


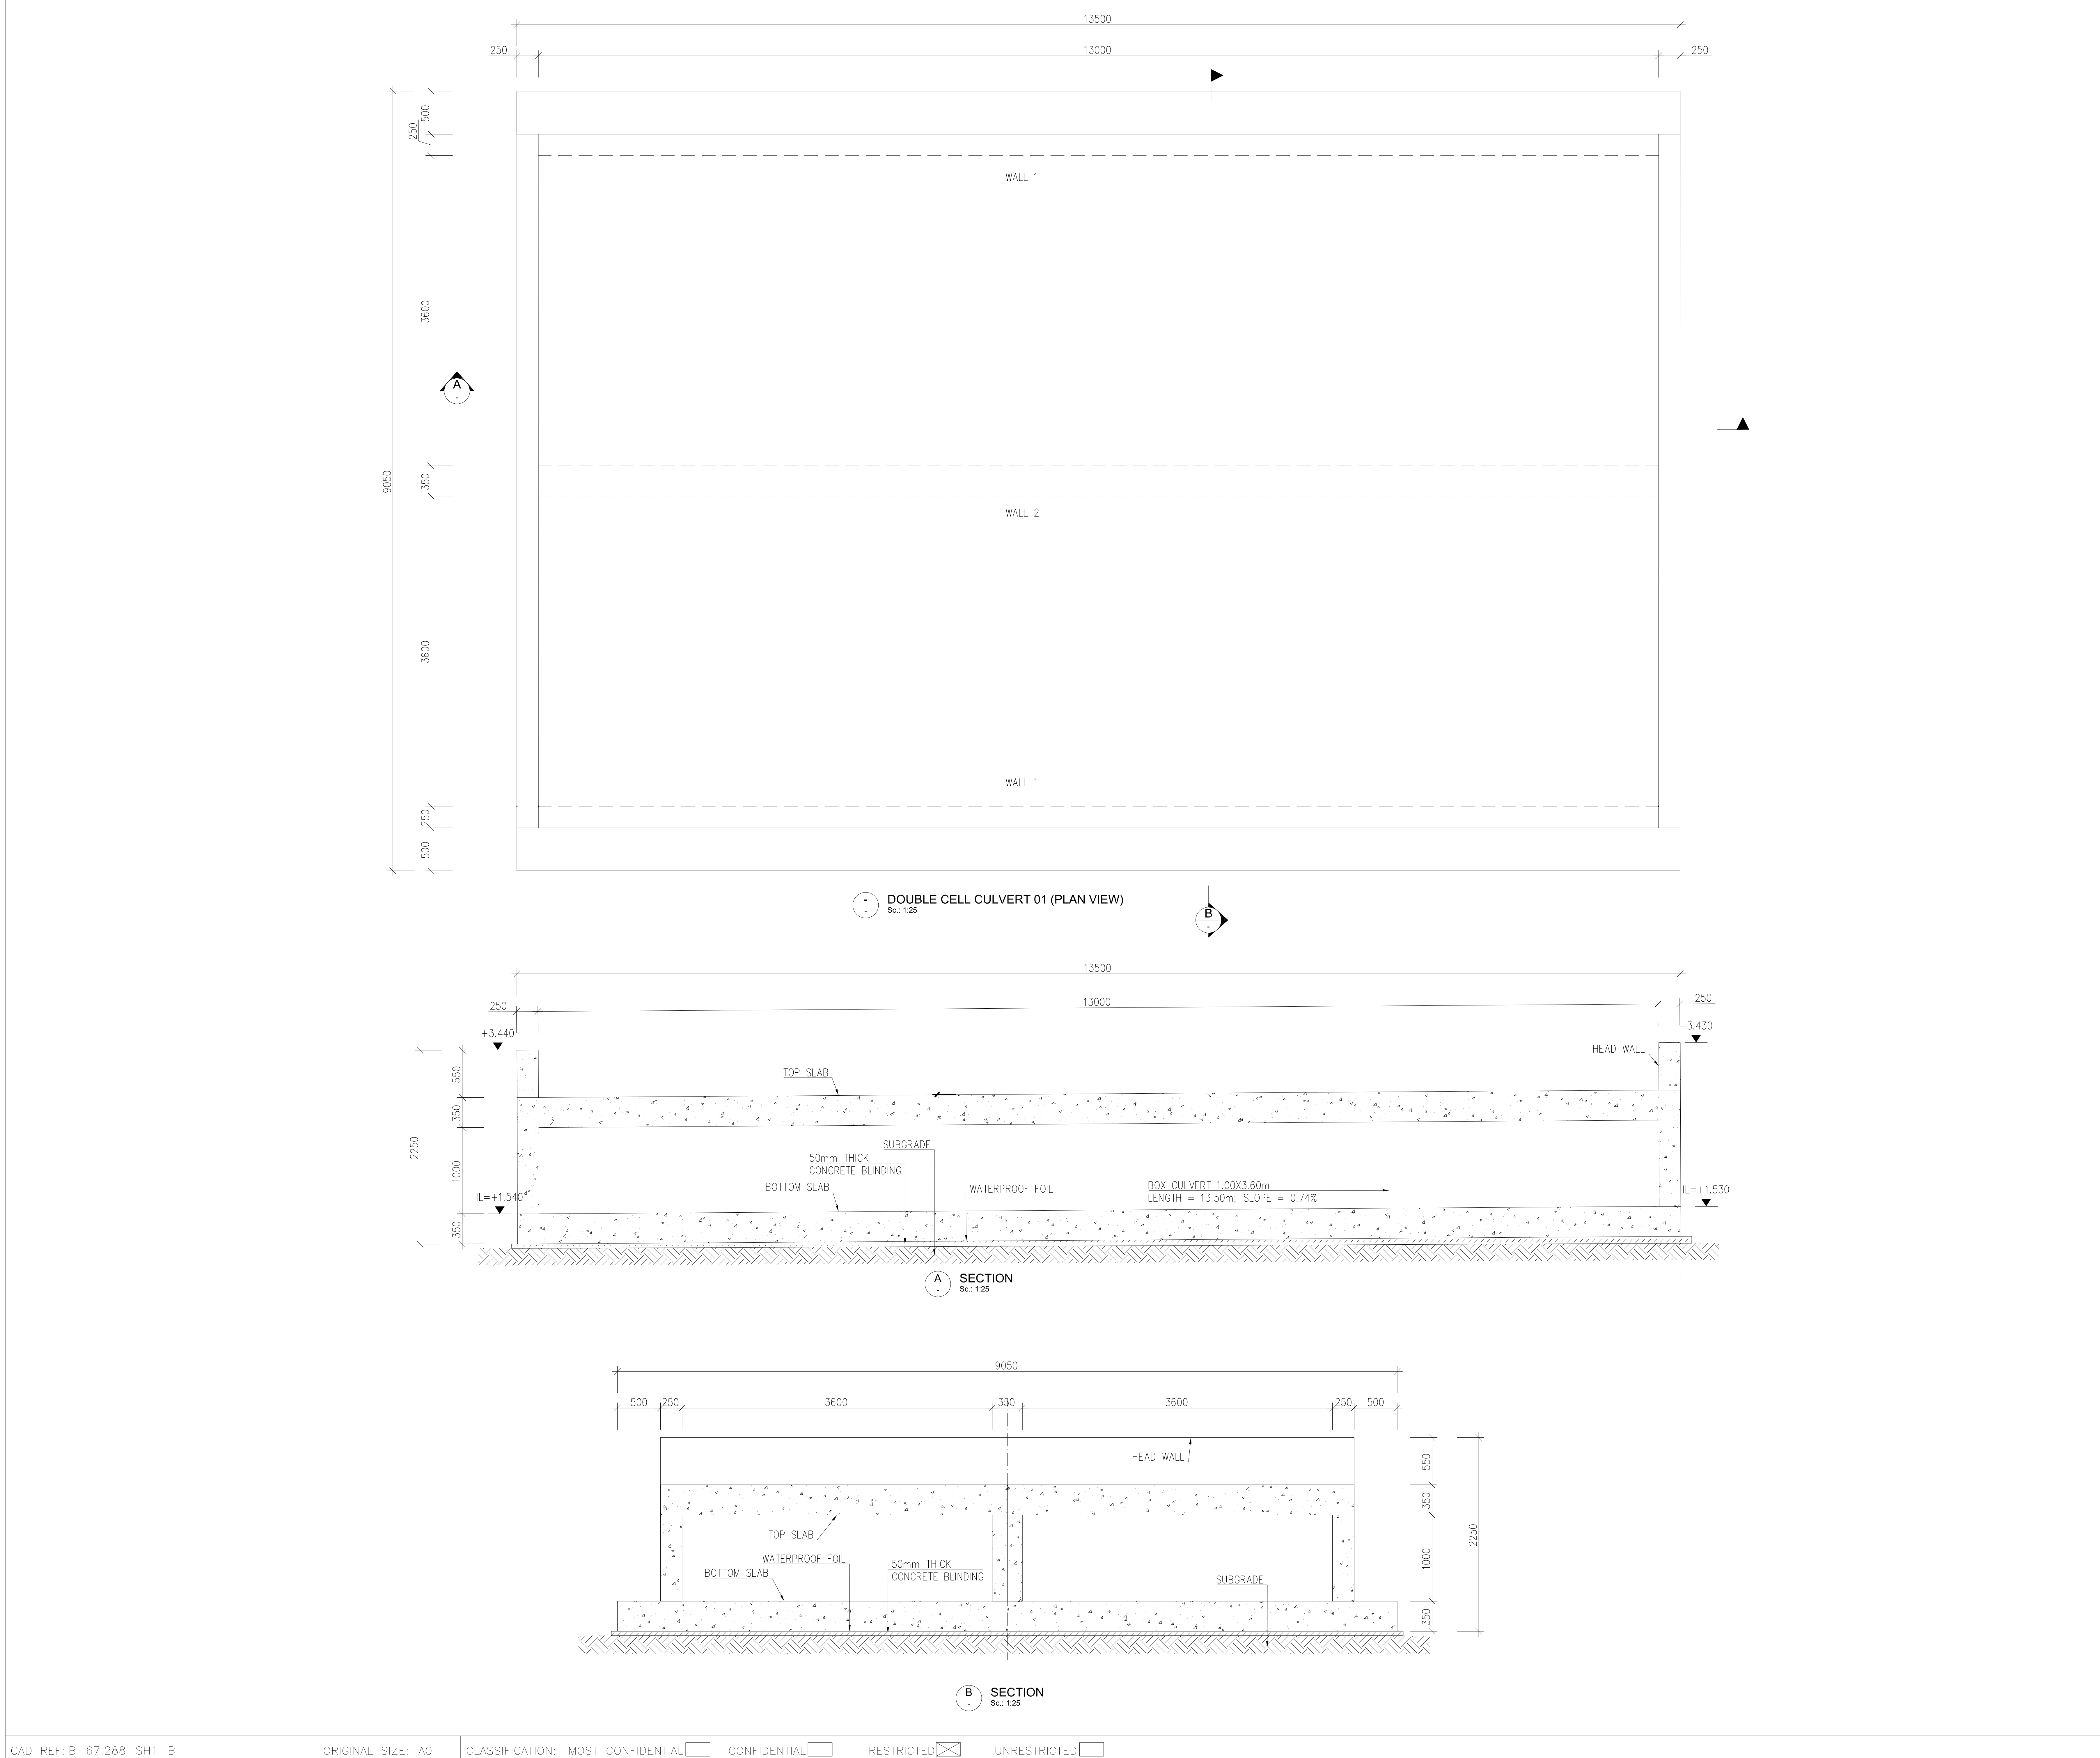

NOTES:

- ALL DIMENSIONS IN MILLIMETERS (mm) AND LEVELS IN METERS (m).
- ALL CONSTRUCTION JIONTS TO BE FINISHED AS ROUGH SURFACES UNLESS STATED OTHERWISE.
- THIS DRAWING MUST BE READ IN CONJUNCTION WITH DRAWING B-67.627
- "UNO" – UNLESS NOTED OTHERWISE

| STRUCTURAL COMPONENT | CLASS OF CONCRETE | GRADE OF REINFORCEMENT | NOMINAL COVER $c_v$ |
|----------------------|-------------------|------------------------|---------------------|
| BOTTOM AND TOP SLAB  | C25/30            | B500B                  | 50 mm               |
| WALLS                | C25/30            | B500B                  | 50 mm               |

BENDING DIMENSIONS GIVEN ON DRAWING ARE OUTSIDE TO OUTSIDE MEASUREMENTS

Diagram showing bending dimensions for a wall and slab. The wall has a thickness of 250 mm. The slab has a thickness of 100 mm. The dimensions are given in terms of the nominal diameter of the reinforcement bars ( $d_s$ ).

| BENDING SCHEDULE – SHEETS (S) |                | MESH SCHEDULE – SHEETS (S) |                |
|-------------------------------|----------------|----------------------------|----------------|
| LAST BAR MARK                 | LAST MESH MARK | LAST BAR MARK              | LAST MESH MARK |
| —                             | —              | —                          | —              |

MINIMUM DIAMETER OF BENDING FORMER  $d_{bf}$  ACCORDING TO BS EN ISO 3766 TABLE 1 AND BS 8666 TABLE 3

| DIAMETER OF BAR       | U-HOOKS L-HOOKS LOOPS STIRRUPS | CONCRETE COVER AT RIGHT ANGLES TO THE PLANE OF CURVATURE | BENT UP AND OTHER CURVED BARS E.G. FRAME CORNER | INNER LAYERS OF BENT-UP AND OTHER CURVED BARS OF MORE THAN ONE LAYER |
|-----------------------|--------------------------------|----------------------------------------------------------|-------------------------------------------------|----------------------------------------------------------------------|
| < $\varnothing 20$    | 4 $d_s$                        | > 5 cm and > 3 $d_s$                                     | 15 $d_s$                                        | 22.5 $d_s$                                                           |
| $\geq \varnothing 20$ | 7 $d_s$                        | $\leq$ 5 cm and $\leq$ 3 $d_s$                           | 20 $d_s$                                        | 30 $d_s$                                                             |

SPACERS: ACCORDING TO DBV-NOTES "SPACERS" (FOR TYPE) AND "CONCRETE COVER" (TAB. 4 FOR ARRANGEMENT)

REFERENCE DRAWINGS

| DRAWING No.: | SUBJECT:           |
|--------------|--------------------|
| B-67.265     | STORMWATER DETAILS |
|              |                    |
|              |                    |
|              |                    |
|              |                    |

DATUM LINE =  $\pm 0.00m$  (FFL) = + 4.05m

Site plan showing the location of the culvert within the industrial area. The culvert is located near the head wall. The plan shows the layout of the culvert and the surrounding area. A north arrow is provided.

| REV | DESCRIPTION               | DWN | DATE    | CHKD | DATE    | APPD | DATE    |
|-----|---------------------------|-----|---------|------|---------|------|---------|
| B   | APPROVED FOR CONSTRUCTION | NU  | 04FEB25 | IO   | 04FEB25 | KH   | 04FEB25 |
| A   | ISSUED FOR APPROVAL       | NU  | 30JAN25 | IO   | 30JAN25 | KH   | 30JAN25 |
| O   | ISSUED FOR COMMENT        | NU  | 28JAN25 | IO   | 28JAN25 | KH   | 28JAN25 |

REVISIONS

This Document is confidential. The copyright therein is vested in Nigeria LNG Ltd, Nigeria. Recipient must obtain the written authority of the said company before wholly or partially duplicating. All rights reserved.

DRAWN: N.UCHENNA  
DATE: 28JAN25  
CHECKED: LOBI  
DATE: 28JAN25  
APPROVED: K.HARUNA  
DATE: 28JAN25  
APPD: LNG:  
DATE:  
CONTRACT CO. DWG. No.: 9500211002  
SCALE: 1:50 UNO

PROJECT: NEW IA WAREHOUSE PROJECT  
LOCATION: NLNG INDUSTRIAL AREA BONNY ISLAND  
DISCIPLINE: CIVIL  
UNIT No.: 8490  
TITLE: REINFORCEMENT DRAWING  
BOX CULVERT 01 FORMWORK AND REINFORCEMENT  
NLNG PROJECT No.: 19/MOC/PDR/014P  
DRAWING No.: B-67.288  
SHEET: 1 OF 2  
REV: B


NIGERIA LIQUEFIED NATURAL GAS

PRIME TECH


CAD REF: B-67.288-SH1-B

ORIGINAL SIZE: A0


CLASSIFICATION: MOST CONFIDENTIAL ☐ CONFIDENTIAL ☐ RESTRICTED ☒ UNRESTRICTED ☐

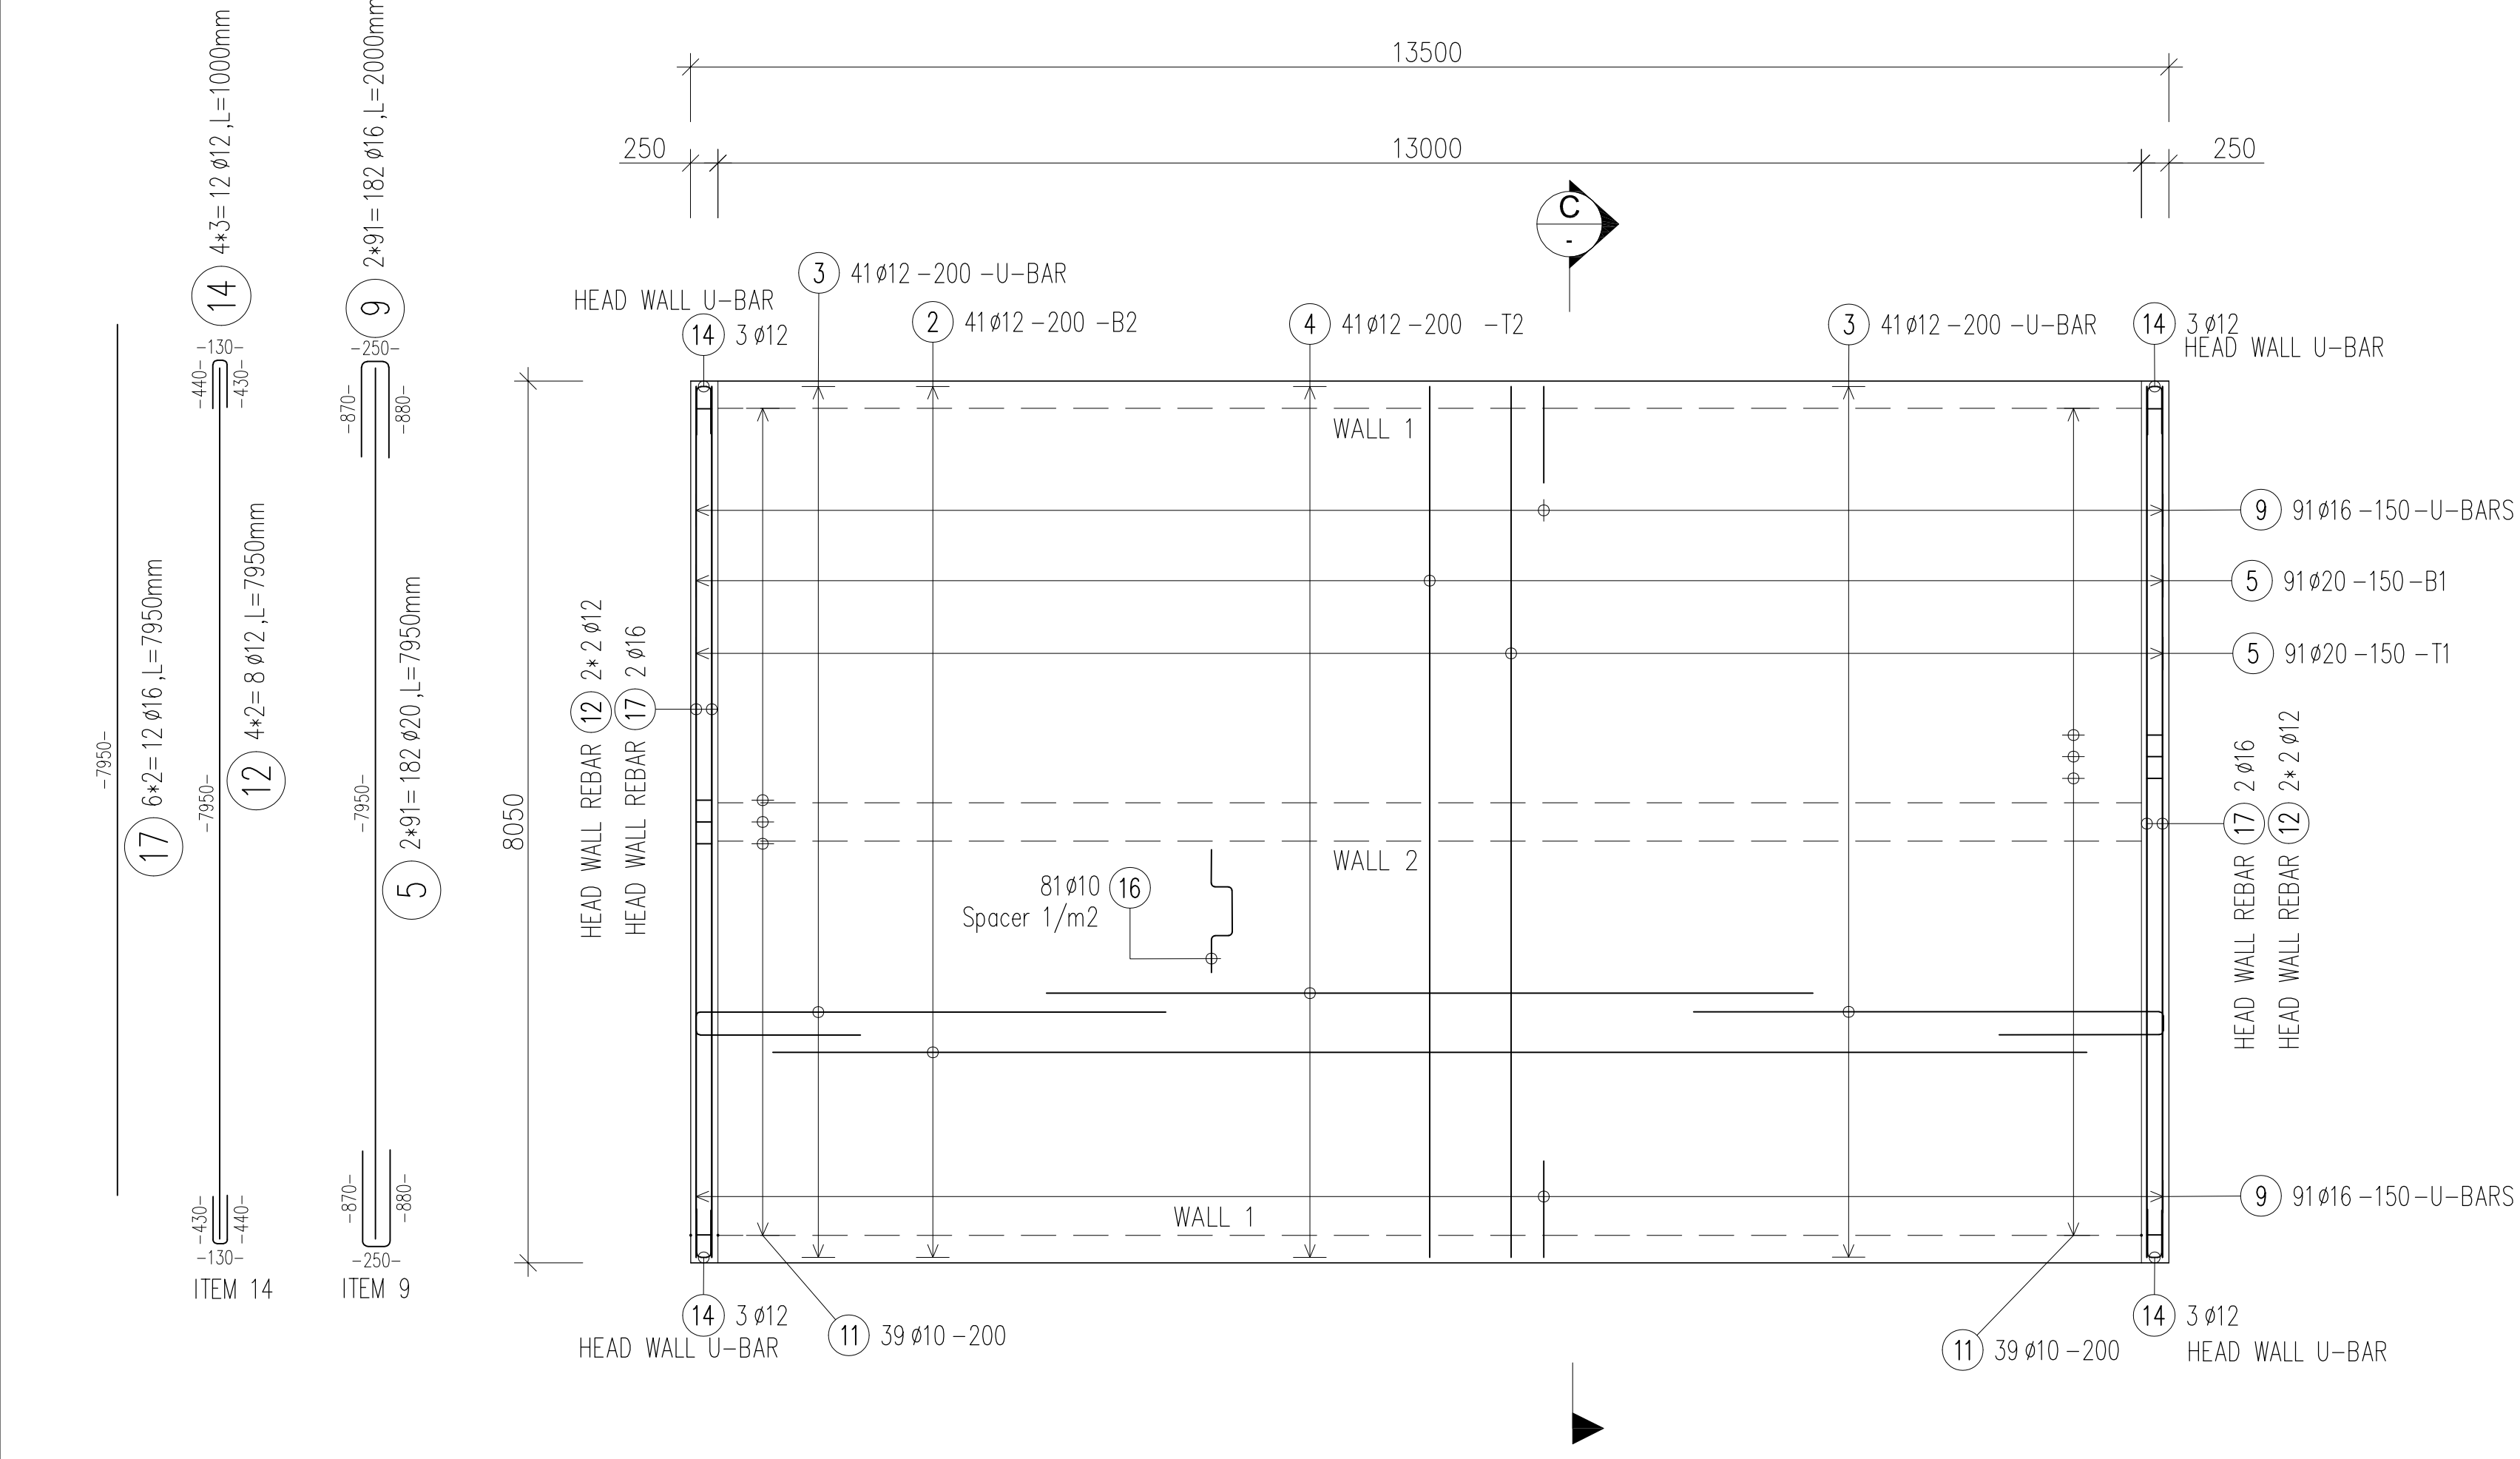


DOUBLE CELL CULVERT 01 (PLAN VIEW)  
TOP SLAB REINFORCEMENT DETAIL

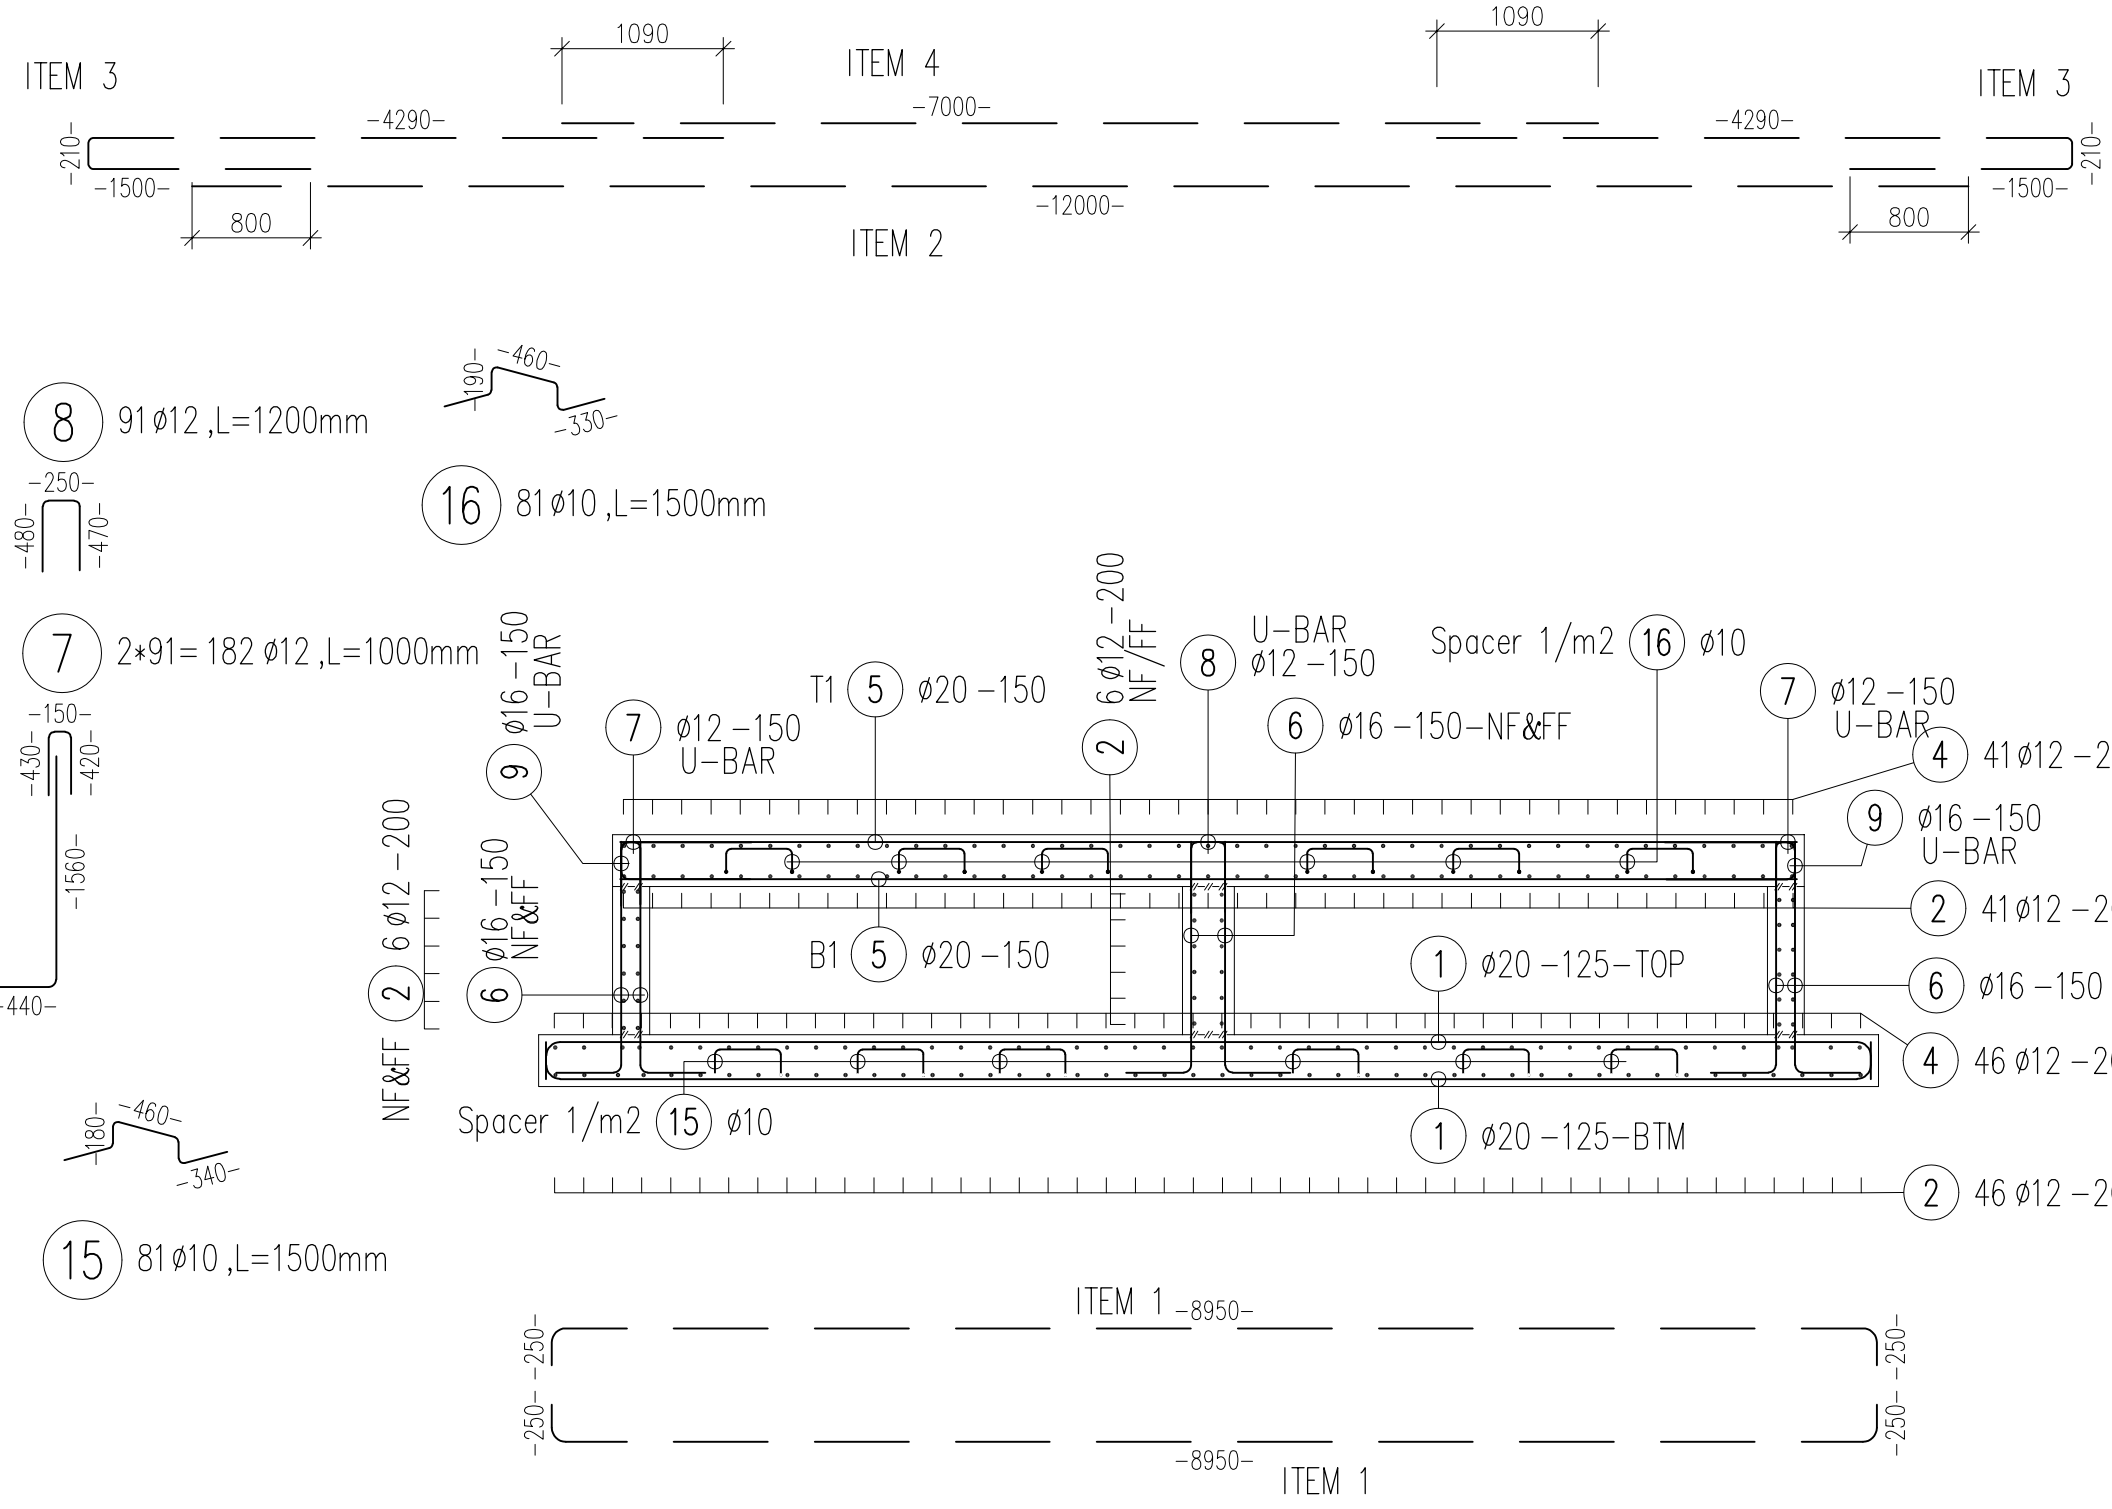


SECTION  
SC: 1:50

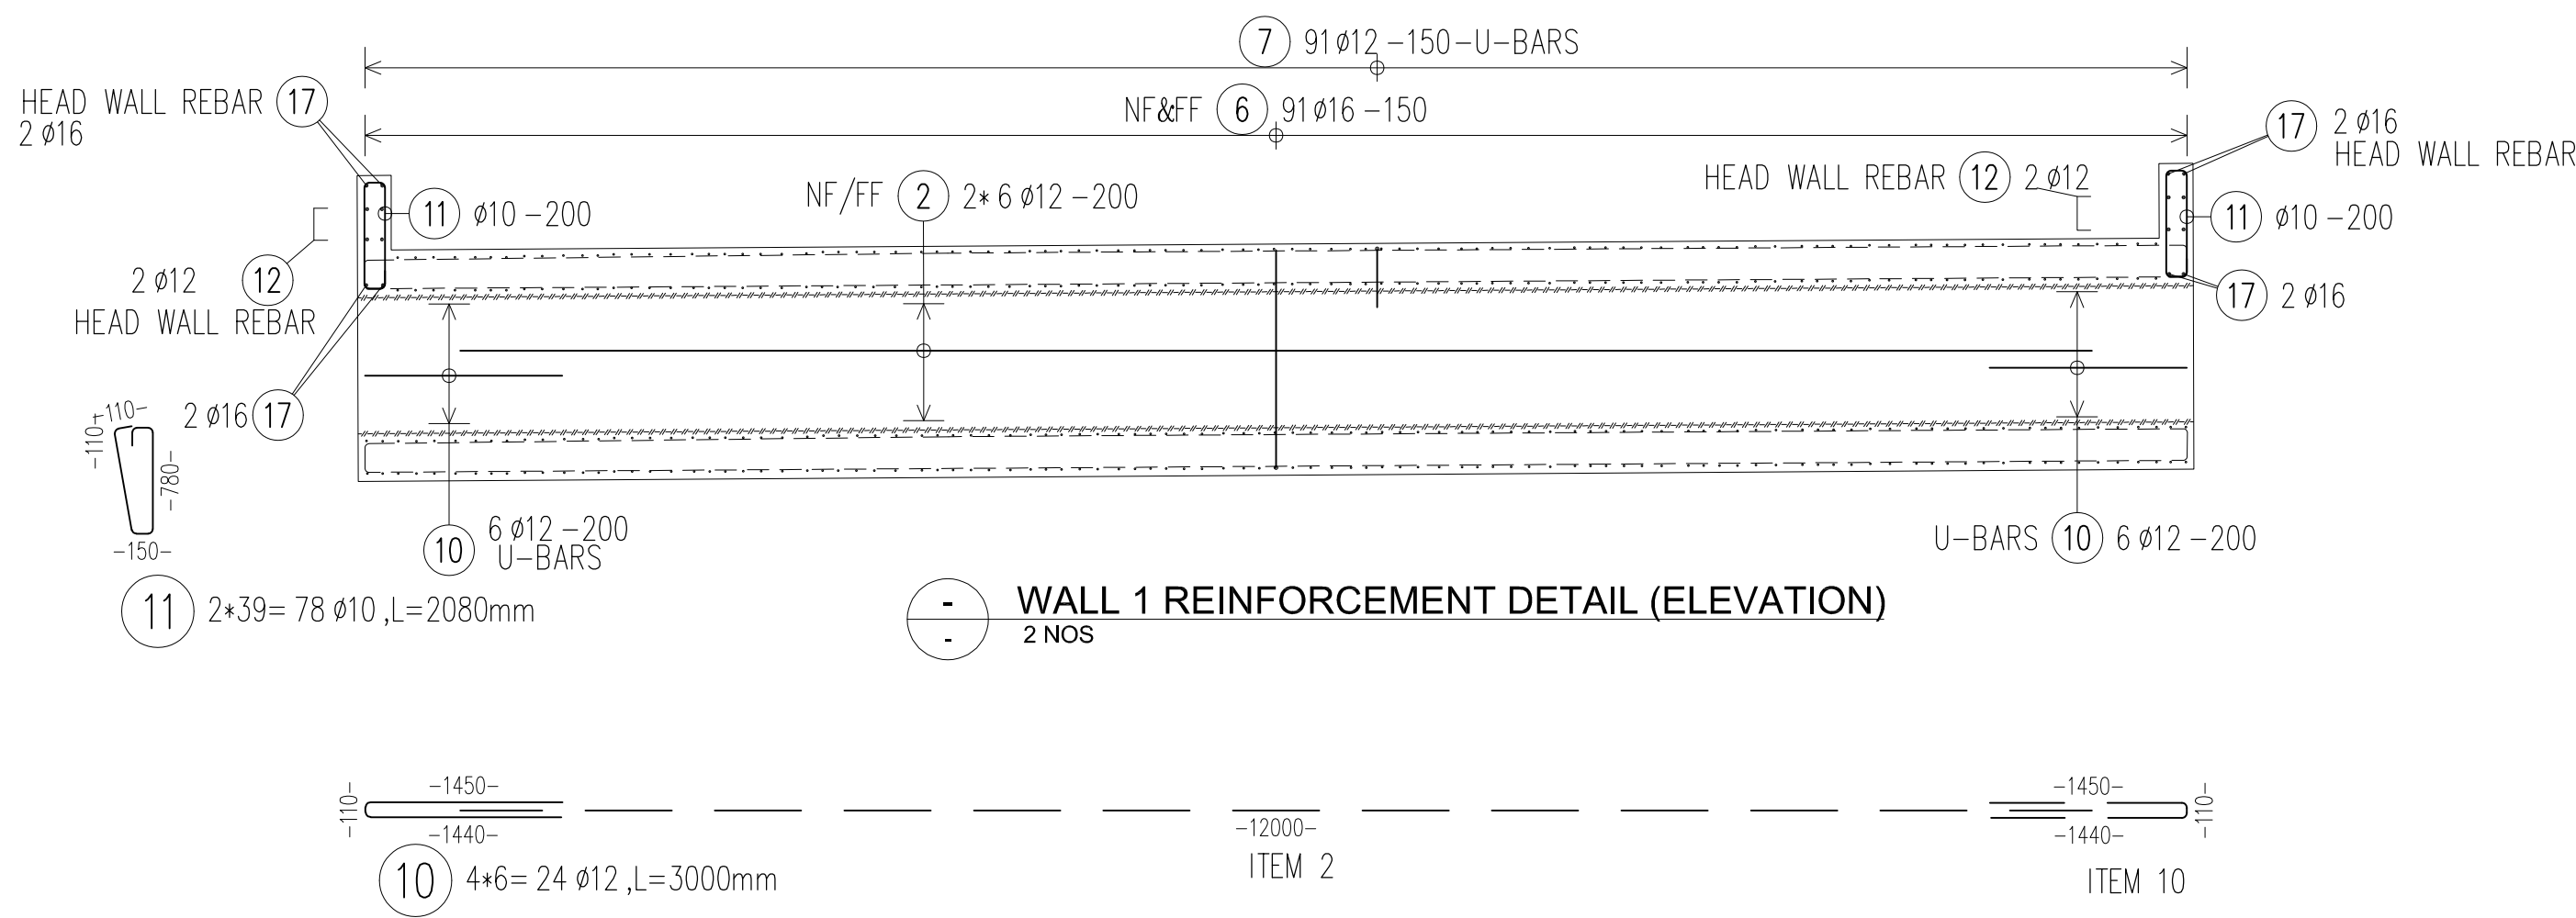


WALL 1 REINFORCEMENT DETAIL (ELEVATION)  
2 NOS

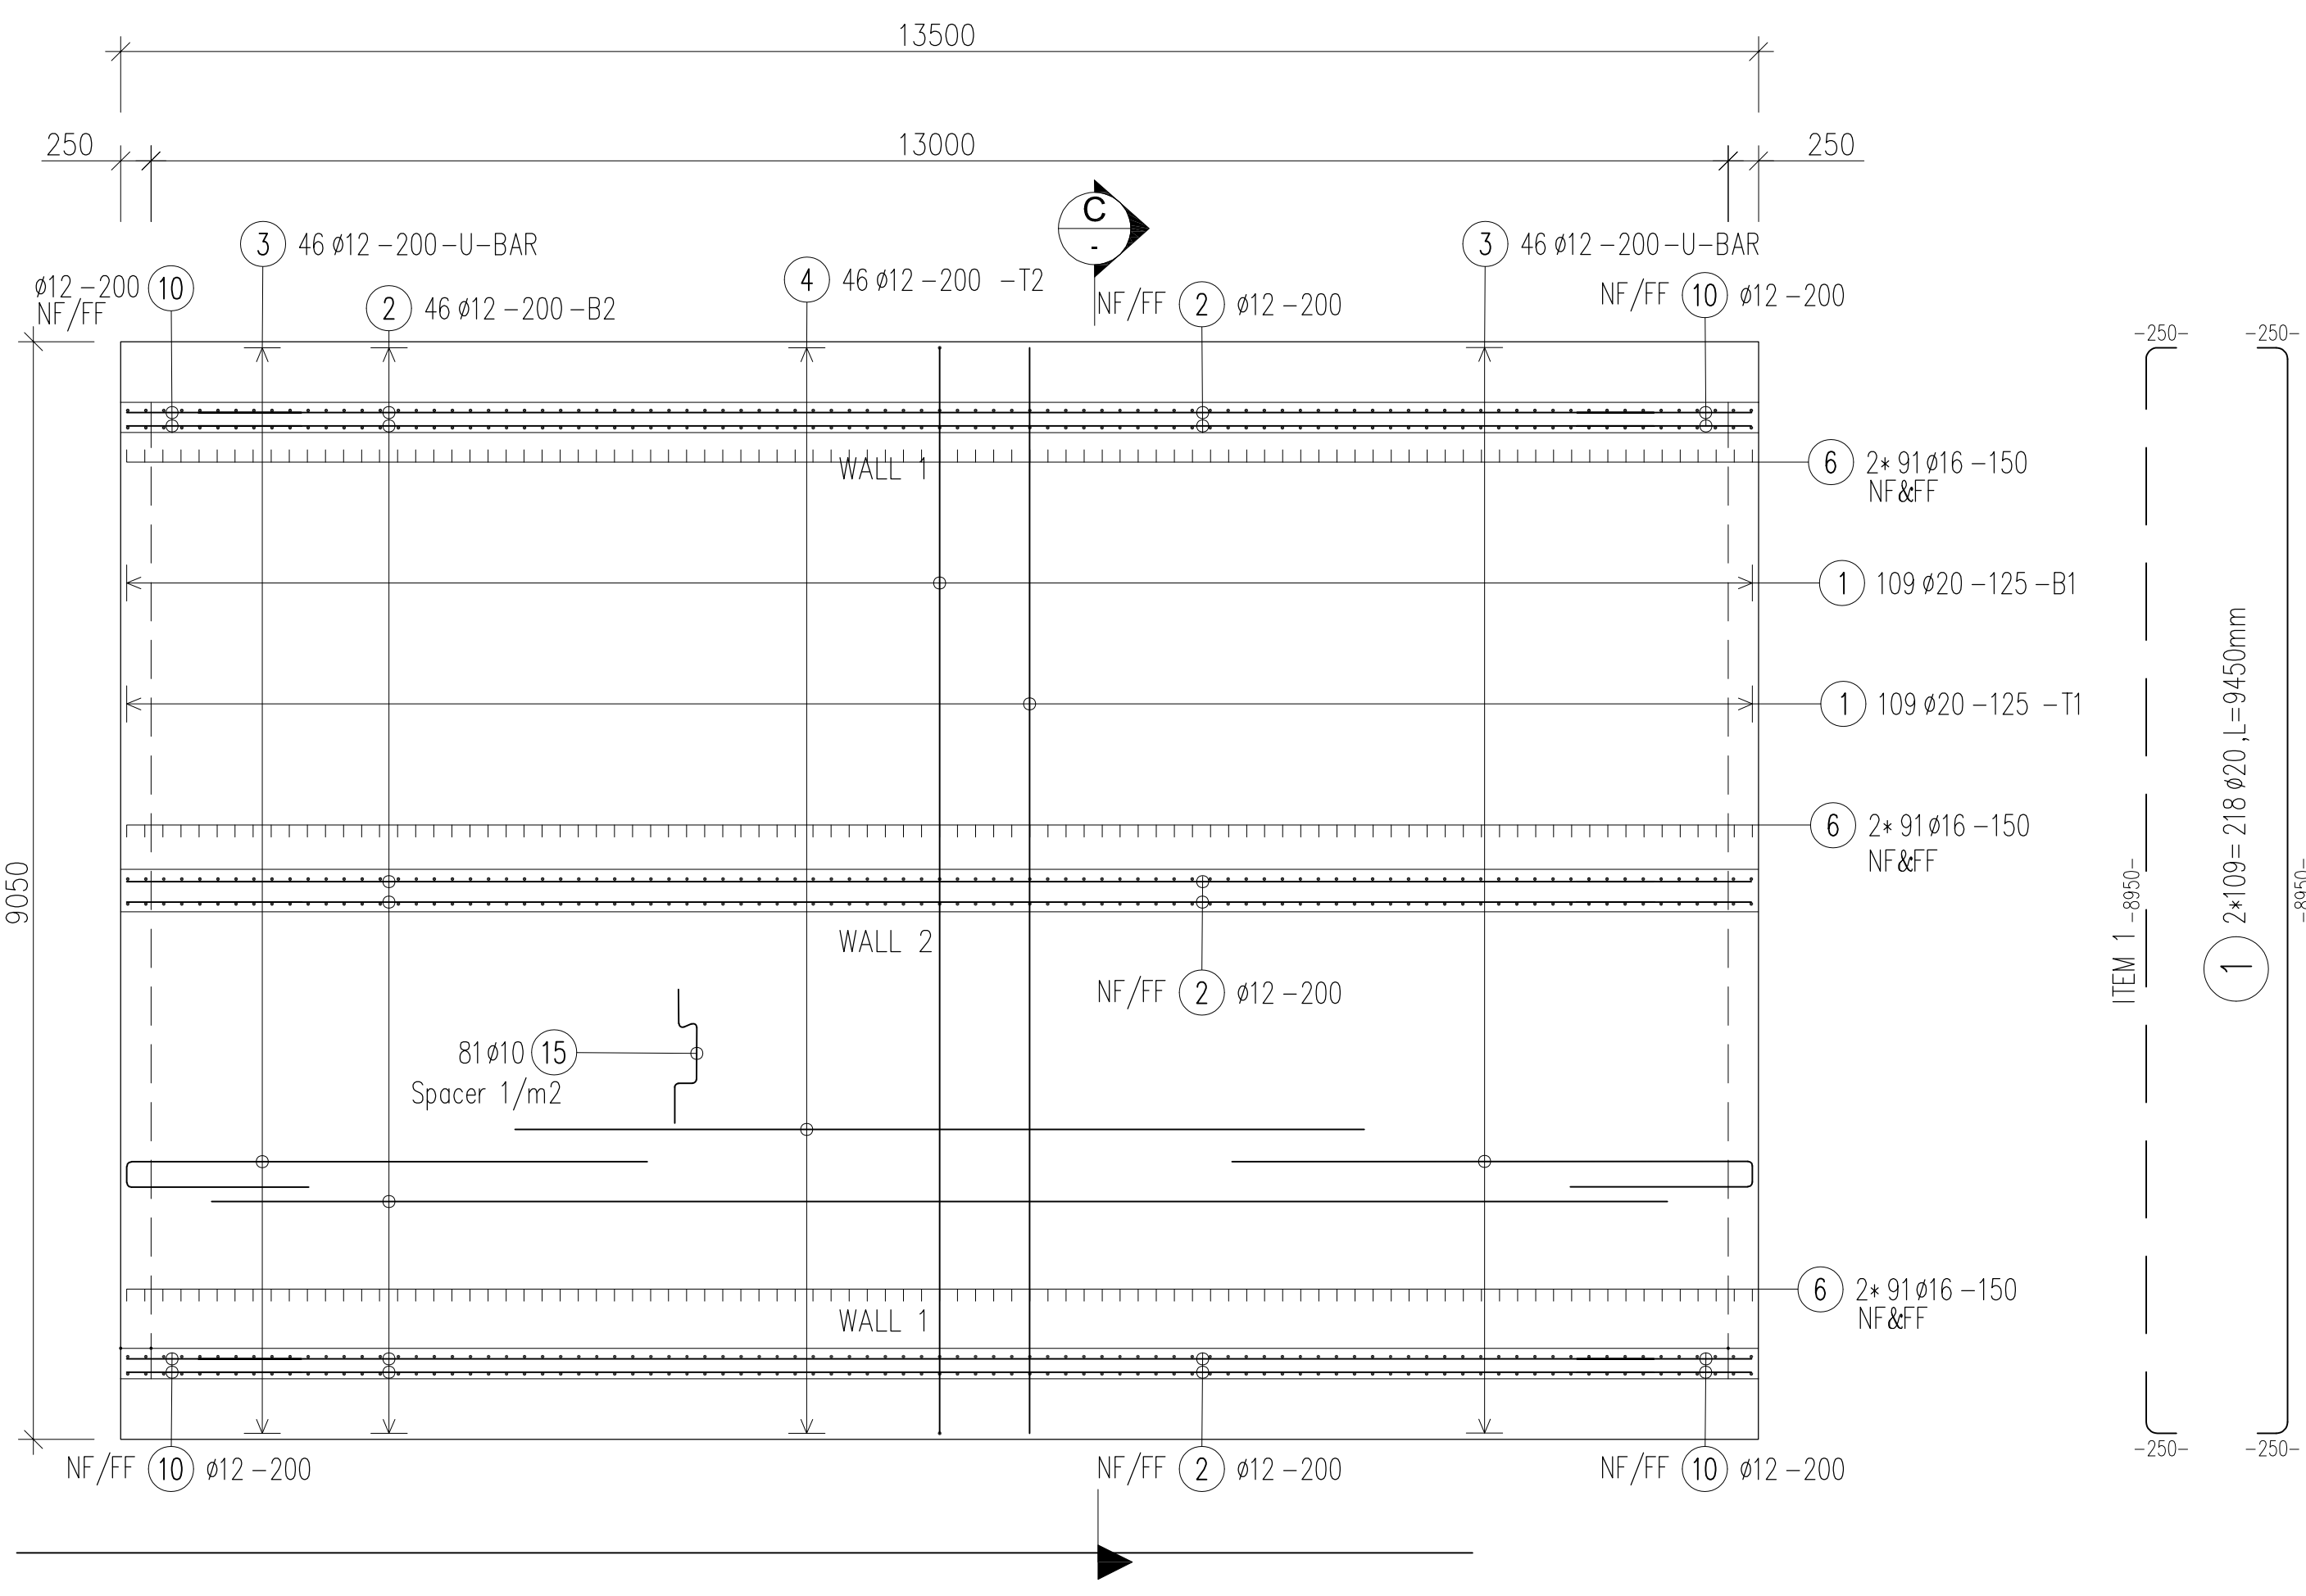


DOUBLE CELL CULVERT 01 (PLAN VIEW)  
BOTTOM SLAB REINFORCEMENT DETAIL

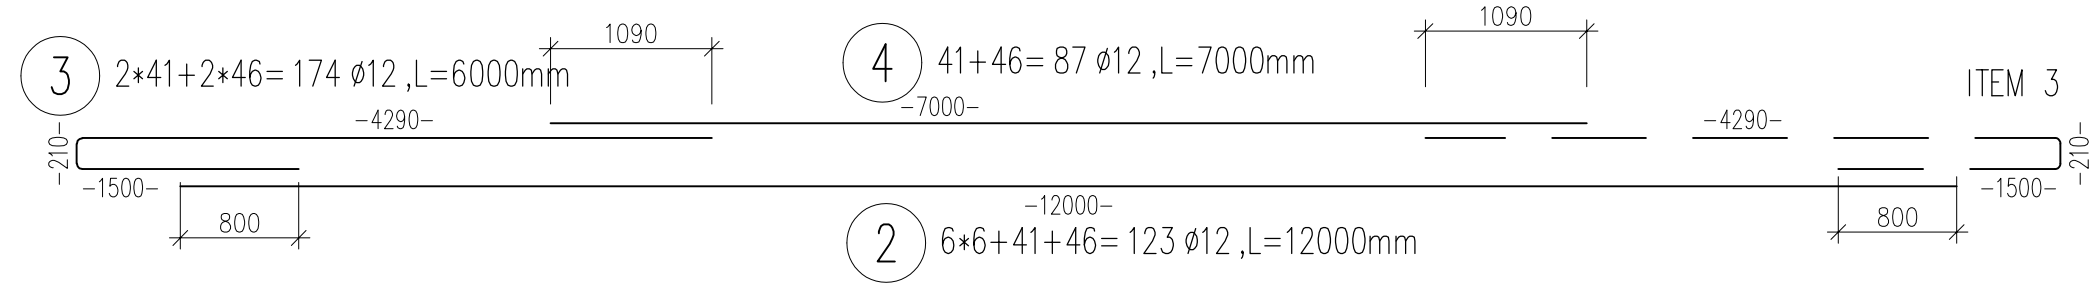


WALL 2 REINFORCEMENT DETAIL (ELEVATION)  
2 NOS

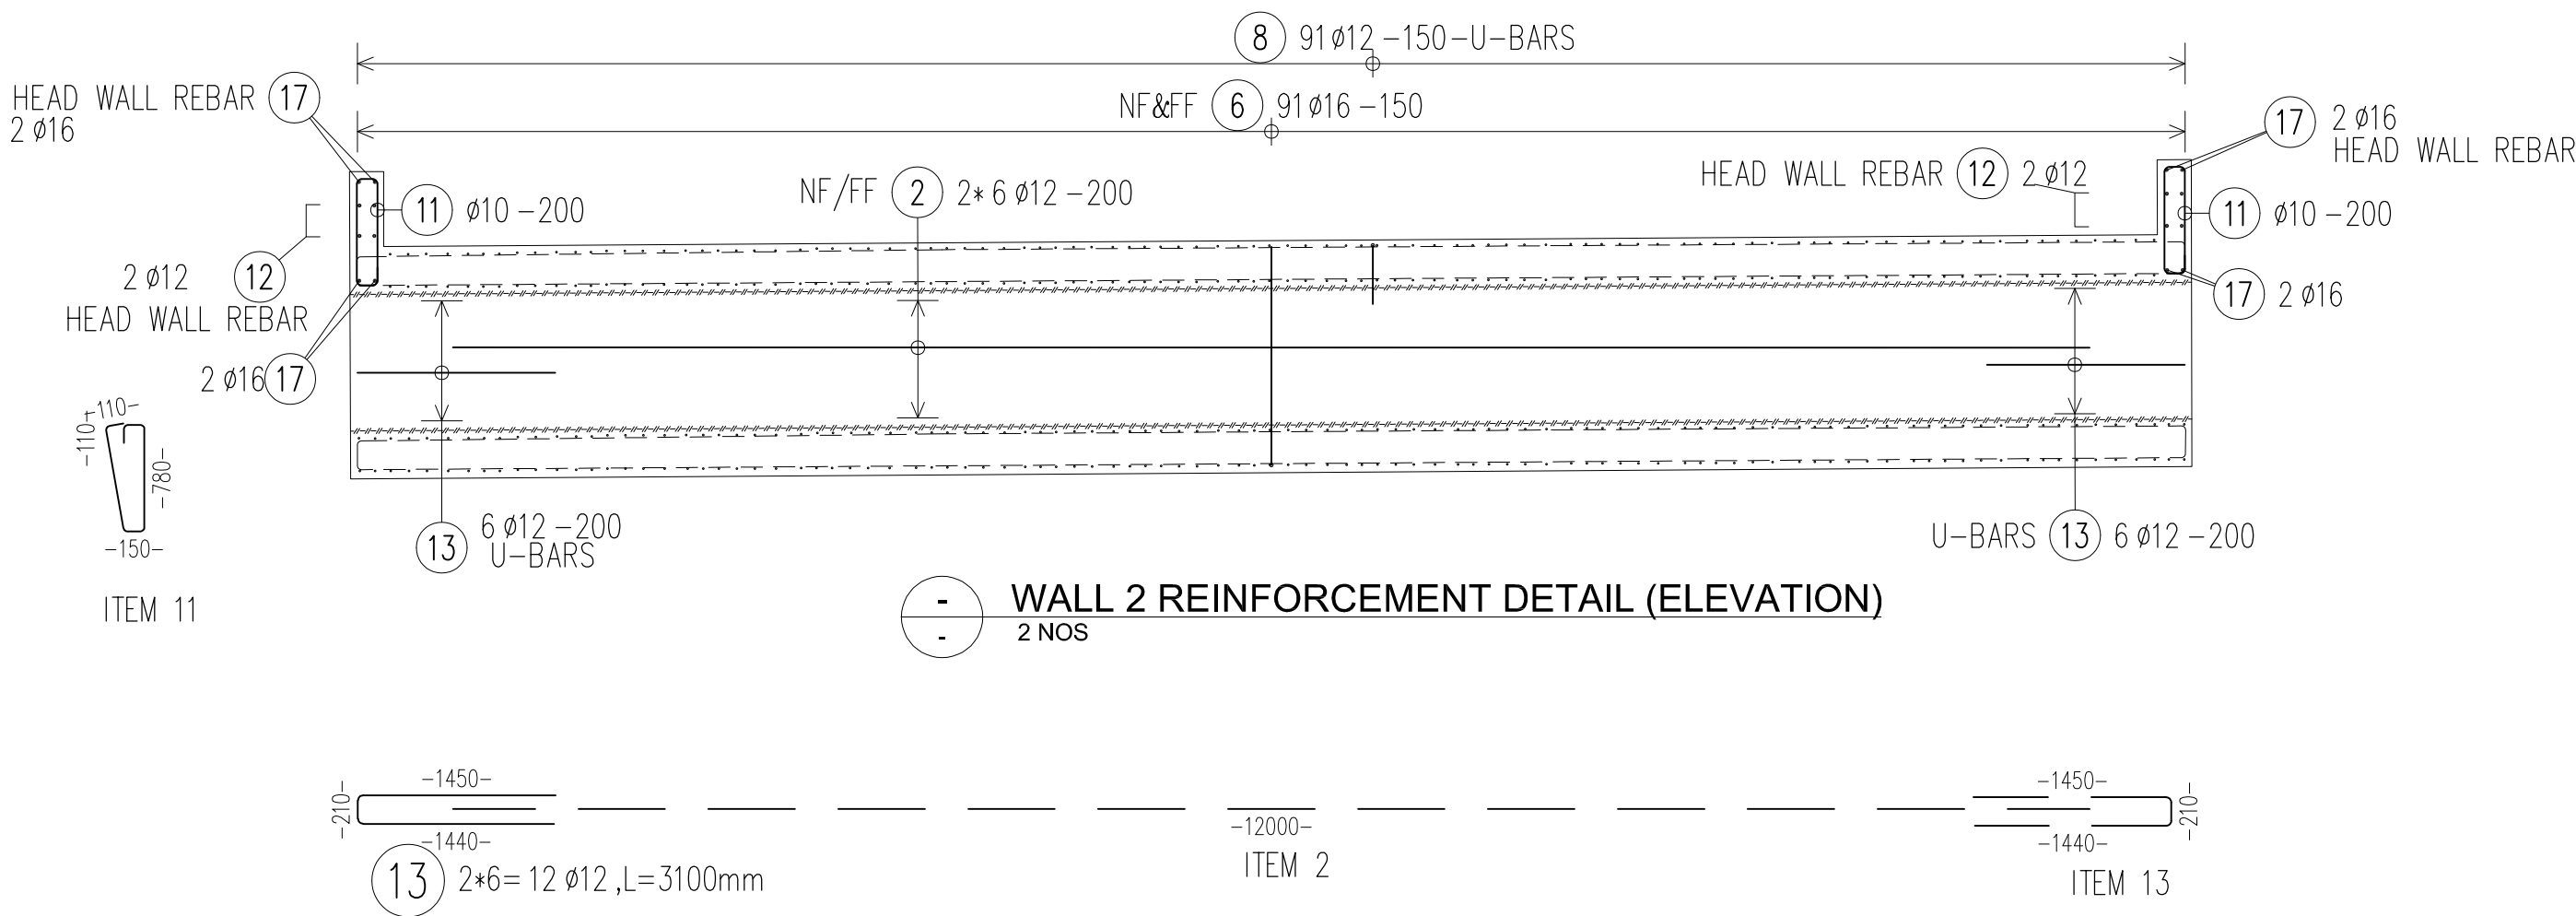

- NOTES:
- ALL DIMENSIONS IN MILLIMETERS (mm) AND LEVELS IN METERS (m).
  - ALL CONSTRUCTION JOINTS TO BE FINISHED AS ROUGH SURFACES UNLESS STATED OTHERWISE.
  - THIS DRAWING MUST BE READ IN CONJUNCTION WITH DRAWING B-67.627
  - "UNO" – UNLESS NOTED OTHERWISE
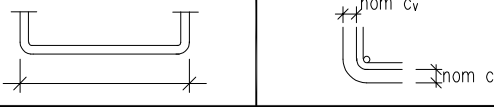
|   |                                         |   |                                                                                     |                                                                      |
|---|-----------------------------------------|---|-------------------------------------------------------------------------------------|----------------------------------------------------------------------|
| STRUCTURAL COMPONENT                                                                               | CLASS OF CONCRETE                       | GRADE OF REINFORCEMENT                                                                              | NOMINAL COVER $c_v$                                                                 |                                                                      |
| BOTTOM AND TOP SLAB WALLS                                                                          | C25/30<br>C25/30                        | B500B<br>B500B                                                                                      | 50 mm<br>50 mm                                                                      |                                                                      |
| BENDING DIMENSIONS GIVEN ON DRAWING ARE OUTSIDE TO OUTSIDE MEASUREMENTS                            |                                         |   |  |                                                                      |
| BENDING SCHEDULE 3 SHEETS (S)                                                                      |                                         | MESH SCHEDULE — SHEETS (S)                                                                          |                                                                                     |                                                                      |
| LAST BAR MARK  |                                         | LAST MESH MARK  |                                                                                     |                                                                      |
| MINIMUM DIAMETER OF BENDING FORMER $d_b$ ACCORDING TO BS EN ISO 3766 TABLE 1 AND BS 8666 TABLE 3   |                                         |   |                                                                                     |                                                                      |
| DIAMETER OF BAR                                                                                    | U-HOOKS<br>L-HOOKS<br>LOOPS<br>STIRRUPS | CONCRETE COVER AT RIGHT ANGLES TO THE PLANE OF CURVATURE                                            | BENT UP AND OTHER CURVED BARS E.G. FRAME CORNER                                     | INNER LAYERS OF BENT-UP AND OTHER CURVED BARS OF MORE THAN ONE LAYER |
| $< \phi 20$                                                                                        | $4d_s$                                  | $> 5$ cm and $> 3d_s$                                                                               | $15d_s$                                                                             | $22.5d_s$                                                            |
| $\geq \phi 20$                                                                                     | $7d_s$                                  | $\leq 5$ cm and $\leq 3d_s$                                                                         | $20d_s$                                                                             | $30d_s$                                                              |
| SPACERS: ACCORDING TO DBV-NOTES "SPACERS" (FOR TYPE) AND "CONCRETE COVER" (TAB. 4 FOR ARRANGEMENT) |                                         |   |                                                                                     |                                                                      |

|                    |                     |
|--------------------|---------------------|
| REFERENCE DRAWINGS |                     |
| DRAWING No.:       | SUBJECT:            |
| B-67.265           | STORM WATER DETAILS |
|                    |                     |
|                    |                     |
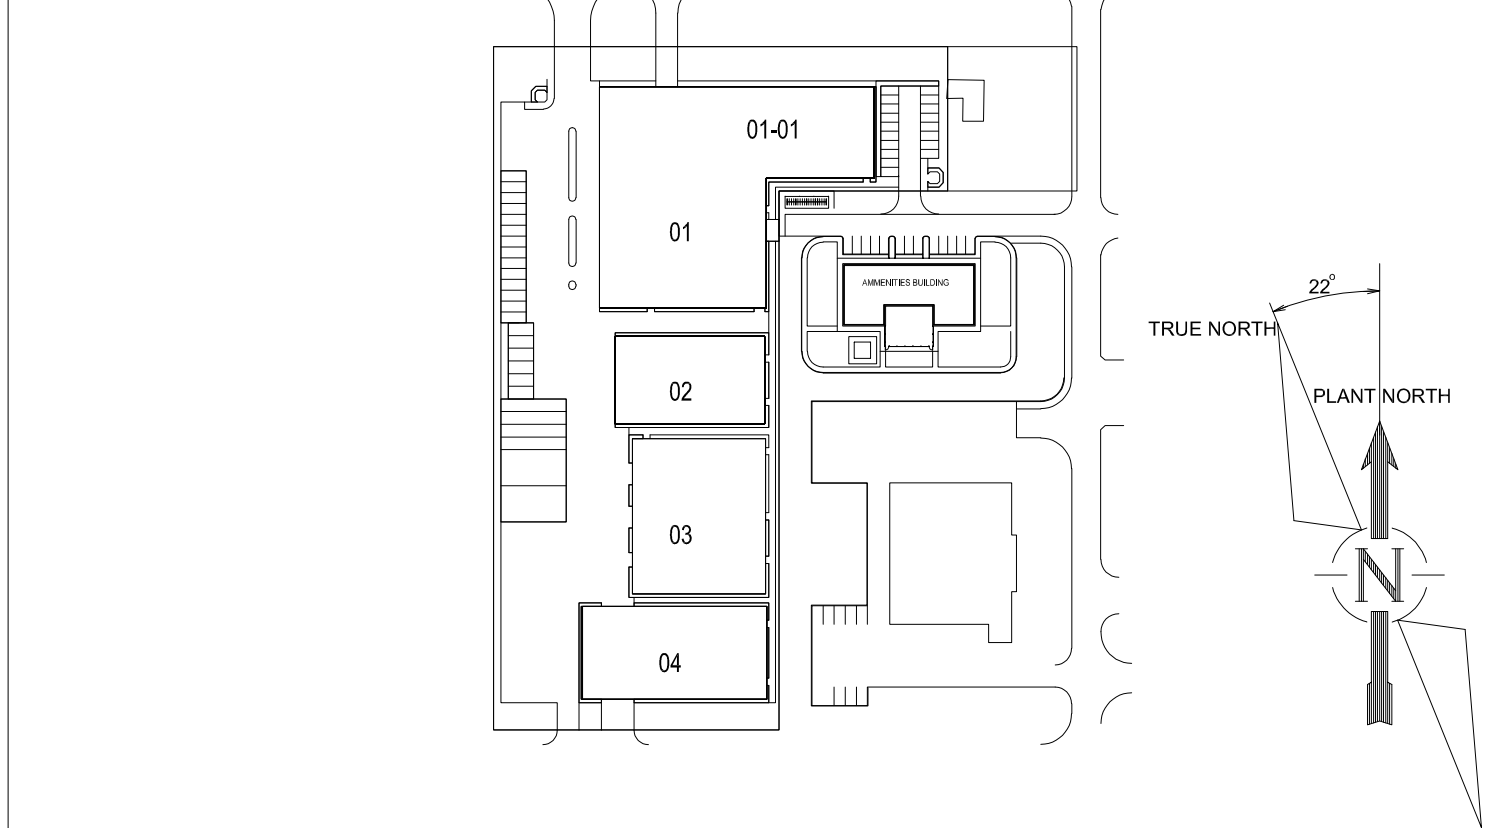

| REV | DESCRIPTION               | DWN | DATE    | CHKD | DATE    | APPD | DATE    |
|-----|---------------------------|-----|---------|------|---------|------|---------|
| B   | APPROVED FOR CONSTRUCTION | NU  | 04FEB25 | IO   | 04FEB25 | KH   | 04FEB25 |
| A   | ISSUED FOR APPROVAL       | NU  | 30JAN25 | IO   | 30JAN25 | KH   | 30JAN25 |
| O   | ISSUED FOR COMMENT        | NU  | 28JAN25 | IO   | 28JAN25 | KH   | 28JAN25 |

|   |   |  |  |
|---|---|--|--|
| This Document is confidential. The copyright therein is vested in Nigeria LNG Ltd, Nigeria. Recipient must obtain the written authority of the said company before wholly or partially duplicating. All rights reserved. |   |  |  |
| DRAWN: N. UCHENNA<br>DATE: 28JAN25<br>CHECKED: LOBI<br>DATE: 28JAN25<br>APPROVED: K. HARUNA<br>DATE: 28JAN25<br>APPD: LNG<br>DATE: 28JAN25<br>CONTRACT CO. DWG. No.: 9500211002                                          | <br><b>NIGERIA LIQUEFIED NATURAL GAS</b><br>PROJECT: NEW 1A WAREHOUSE PROJECT<br>LOCATION: NLNG INDUSTRIAL AREA BONNY ISLAND<br>DISCIPLINE: CIVIL<br>UNIT No.: 8490<br>TITLE: REINFORCEMENT DRAWING<br>BOX CULVERT 01 FORMWORK AND REINFORCEMENT<br>NIG PROJECT No.: 19/MOC/PDR/014P<br>DRAWING No.: B-67.288<br>SHEET: 2 OF 2<br>REV: B |  |  |