


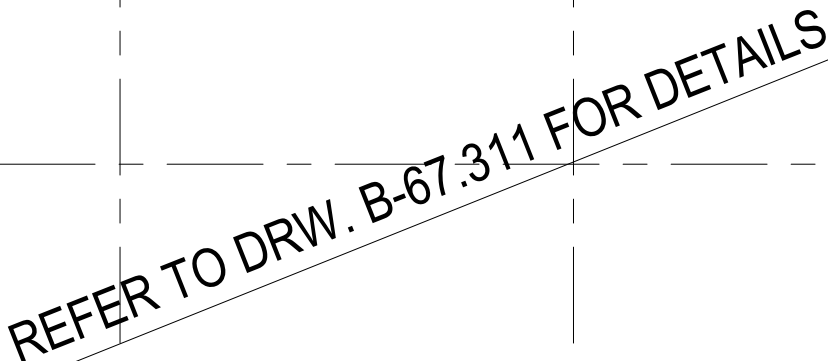

| S/N | FOUNDATION TYPE     | FOOTING SIZE (mm) | PLINTH SIZE (mm) |
|-----|---------------------|-------------------|------------------|
| 1   | FT 01, FT01a, FT01b | 3900x3900x500     | 1300x1300x1250   |
| 2   | FT 02               | 3500x3500x500     | 1200x1200x1250   |
| 3   | FT 03               | 3200x2400x500     | 1000x1000x1250   |
| 4   | FT 04               | 3900x3900x500     | 1500x1300x1250   |
| 5   | FT 05, FT05a        | 3900x3900x500     | 2150x1800x1250   |
| 6   | FT 06               | 3900x3900x500     | 1800x1800x1250   |
| 7   | FT 07               | 3500x3500x500     | 1200x1600x1250   |


| <p>HMS 25/15 concrete</p> <p>HMS 25/15 GENERALLY AT ALL CONNECTIONS BETWEEN CONCRETE AND BRICKWORK IS ALSO ARCHITECTURAL DRAWING</p> <p>EXPOSED CONCRETE GENERALLY (WITHOUT FOUNDATIONS)</p> |                   |                        |                     |
|---|-------------------|------------------------|---------------------|
| STRUCTURAL COMPONENT   | CLASS OF CONCRETE | GRADE OF REINFORCEMENT | NOMINAL COVER $c_n$ |
| FOOTING (TOP/STM)   | C25/30            | B500B                  | 40mm                |
| GROUND SLAB   | C25/30            | B500B                  | 40mm                |
| GROUND BEAM   | C25/30            | B500B                  | 40mm                |
| PLINTH   | C25/30            | B500B                  | 40mm                |

| REFERENCE TO DRAWINGS |                                                        |
|-----------------------|--------------------------------------------------------|
| DRAWING-NO.           | TITLE                                                  |
| B-67.367              | GROUND FLOOR AND SECTIONS                              |
| B-67.311              | NEW IA WAREHOUSE - FOUNDATION LAYOUT - RACKING STORAGE |
| B-67.301              | GROUND FLOOR LAYOUT                                    |
| B-67.261              | SITE FINISHED LEVELS LAYOUT                            |
| B-67.429              | GROUND FLOOR COLUMN REINFORCEMENT                      |
| B-67.384              | MASONRY WALL FRAMING                                   |
| B-67.383              | MASONRY WALL FRAMING                                   |
| B-67.375              | GROUND BEAMS REINFORCEMENT                             |
| B-67.373              | PAD FOUNDATION REINFORCEMENT                           |

**DATUM LINE =  $\pm 0.00\text{m}$  (FFL) =  $3.5\text{m}$**

## OVERVIEW

01-01- NEW WAREHOUSE- RACKING  
STORAGE  
01- NEW WAREHOUSE  
02- LUBE BAY  
03- CHEMICAL STORE & GAS CAGE  
04- SHED OVER SLAB

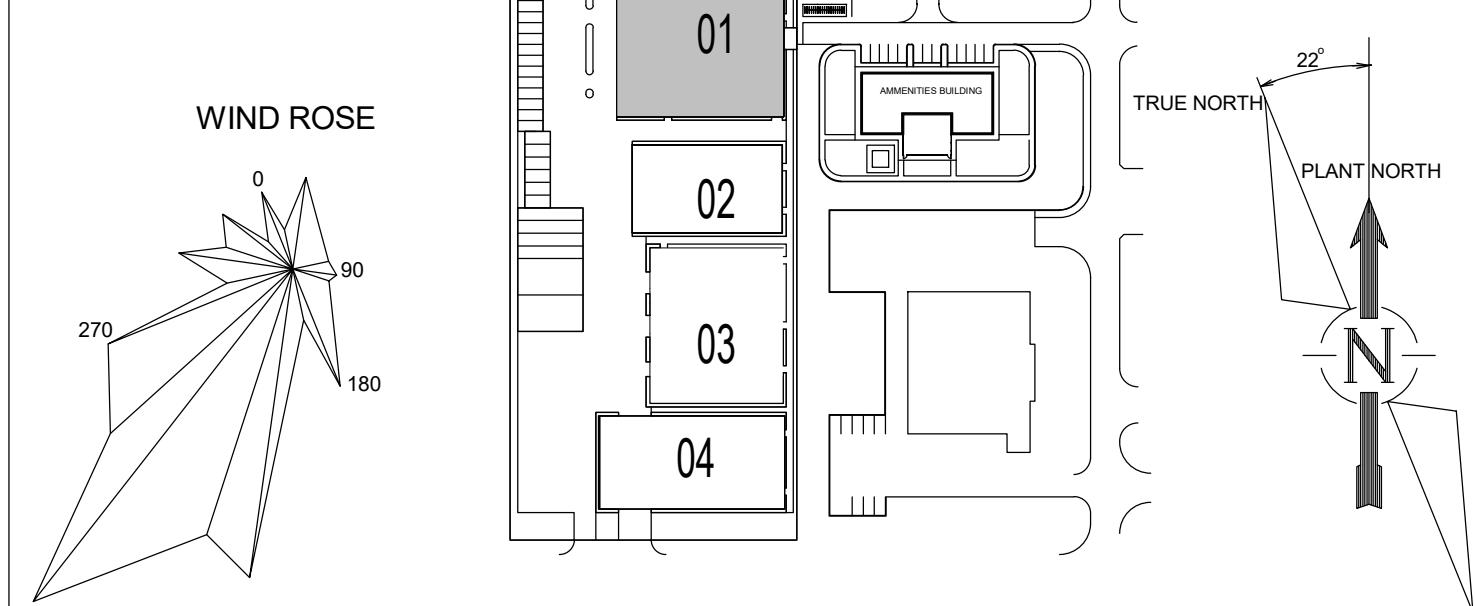

|     |                           |     |           |      |         |      |         |
|-----|---------------------------|-----|-----------|------|---------|------|---------|
|     |                           |     |           |      |         |      |         |
|     |                           |     | AH        |      |         | OS   |         |
| BA  | AFC UPDATED               | AH  | 27NOV24   | OS   | 27NOV24 | KH   | 27NOV24 |
| B   | APPROVED FOR CONSTRUCTION | AH  | 06NOV24   | OS   | 06NOV24 | KH   | 06NOV24 |
| A   | ISSUED FOR APPROVAL       | AH  | 10SEP24   | OS   | 10SEP24 | KH   | 10SEP24 |
| O   | ISSUED FOR COMMENT        | AH  | 17MAY24   | OS   | 17MAY24 | KH   | 17MAY24 |
| REV | DESCRIPTION               | DWN | DATE      | CHKD | DATE    | APPD | DATE    |
|     |                           |     | REVISIONS |      |         |      |         |

This Document is confidential. The copyright therein is vested in Nigeria LNG Ltd, Nigeria.  
Recipient must obtain the written authority of the said company before wholly or partially duplicating.  
All rights reserved.

|   |   |   |
|---|---|---|
| DRAWN: A.HAMBALE<br>DATE: 17MAY24<br>CHECKED: O.SAHEED<br>DATE: 17MAY24<br>APPROVED: K.HARUNA<br>DATE: 17MAY24<br>APPD. LING: |  <b>NIGERIA LIQUEFIED NATURAL GAS</b><br>PROJECT:<br>NEW LIQ WAREHOUSE PROJECT<br>LOCATION:<br>NLNG INDUSTRIAL AREA BONNY ISLAND<br>TITLE:<br>FOUNDATIONS DRAWING – GENERAL<br>FOUNDATION AND SECTIONS |  DISCIPLINE: CIVIL<br>UNIT NO: 8490 |
| DATE: CONTRACT C.O. DWG. NO.                                                                                                  | SCALE: 1:100, U.N.O.<br>NLNG PROJECT NO: 19/MOC/PDR/014P<br>DRAWING NO: B-67.366<br>SHEET: 1 OF 2<br>REV: A   |   |

ALL STEELWORKS DIMENSIONS AND DETAILS SHALL BE READ FROM THE DRAWINGS LISTED BELOW

FOR DETAILED STEELWORKS CONNECTIONS AND SPECIFICATIONS, KINDLY REFER TO THE FOLLOWING DRAWINGS:

- \* B-67.386
- \* B-67.387
- \* B-67.389
- \* B-67.406
- \* B-67.407
- \* B-67.408
- \* B-67.409
- \* B-67.410
- \* B-67.411
- \* B-67.412
- \* B-67.413
- \* B-67.416
- \* B-67.417
- \* B-67.418
- \* B-67.419

### LEGEND

|  |                                  |  |                       |
|--|----------------------------------|--|-----------------------|
|  | NEW CONCRETE                     |  | TOP OF CONCRETE       |
|  | PRECAST CONCRETE                 |  | TOP OF FINISH CONCR.  |
|  | LEAN CONCRETE                    |  | TOP OF CONCRETE       |
|  | CONCR. TO BE CAST LATER          |  | TOP OF FINISH CONCR.  |
|  | MASONRY                          |  | CONSTRUCTION JOINT    |
|  | CONCRETE MASONRY                 |  | ANCHORING RAILS       |
|  | SAND FILL OR MORTAR SETTING BED  |  | EARTH WIRE            |
|  | OPENINGS IN WALLS                |  | STRIP STEEL           |
|  | OPENINGS IN SLABS                |  | 30x3.5 BUILT IN PARTS |
|  | BAR GRATING                      |  | TOP LEVEL             |
|  | CHECKERED PLATE                  |  | BOTTOM LEVEL          |
|  | BOX FOR REINFORCEMENT CONNECTION |  | WALL SLOT             |
|  | DETAIL FOR CONCRETE EDGES        |  | FLOOR OPENING         |
|  | WORKING JOINT                    |  | CEILING OPENING       |
|  | CONTRACTION JOINT                |  | WALL OPENING          |
|  |                                  |  | INVERT LEVEL          |
|  |                                  |  | CENTER LINE           |

HMS 25/15 GENERALLY AT ALL CONNECTIONS BETWEEN CONCRETE AND BRICKWORK SEE ALSO ARCHITECTURAL DRAWING

| EXPOSED CONCRETE GENERALLY (WITHOUT FOUNDATIONS) |                   |                        |                     |  |
|--------------------------------------------------|-------------------|------------------------|---------------------|--|
| STRUCTURAL COMPONENT                             | CLASS OF CONCRETE | GRADE OF REINFORCEMENT | NOMINAL COVER $c_n$ |  |
| FOOTING (TOP/BTM)                                | C25/30            | B500B                  | 40mm                |  |
| GROUND SLAB                                      | C25/30            | B500B                  | 40mm                |  |
| GROUND BEAM                                      | C25/30            | B500B                  | 40mm                |  |
| PLINTH                                           | C25/30            | B500B                  | 40mm                |  |


REFERENCE TO DRAWINGS

| DRAWING-NO. | TITLE                                                  |
|-------------|--------------------------------------------------------|
| B-67.367    | GROUND FLOOR AND SECTIONS                              |
| B-67.311    | NEW IA WAREHOUSE - FOUNDATION LAYOUT - RACKING STORAGE |
| B-67.301    | GROUND FLOOR LAYOUT                                    |
| B-67.261    | SITE FINISHED LEVELS LAYOUT                            |
| B-67.429    | GROUND FLOOR COLUMN REINFORCEMENT                      |
| B-67.384    | MASONRY WALL FRAMING                                   |
| B-67.383    | MASONRY WALL FRAMING                                   |
| B-67.375    | GROUND BEAMS REINFORCEMENT                             |
| B-67.373    | PAD FOUNDATION REINFORCEMENT                           |

**DATUM LINE =  $\pm 0.00\text{m}$  (FFL) =  $3.5\text{m}$**

## OVERVIEW


01-01- NEW WAREHOUSE- RACKING  
STORAGE  
01- NEW WAREHOUSE  
02- LUBE BAY  
03- CHEMICAL STORE & GAS CAGE  
04- SHED OVER SLAB

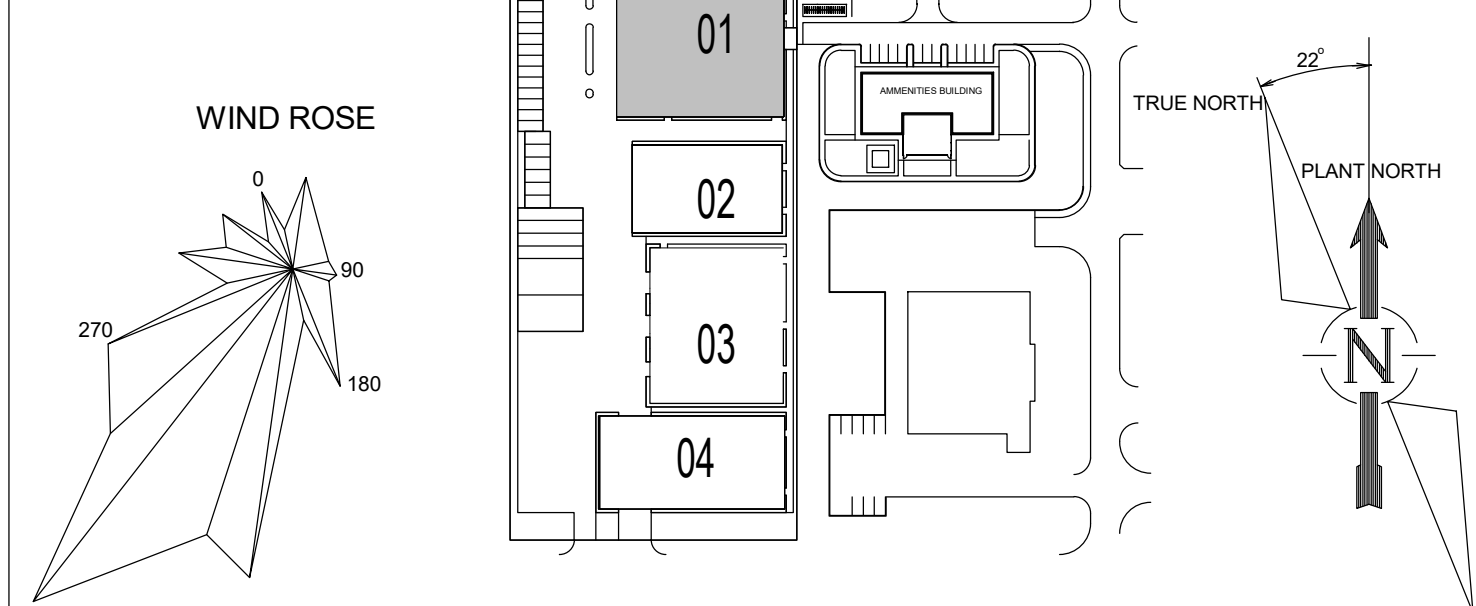[illegible]

This Document is confidential. The copyright therein is vested in Nigeria LNG Ltd, Nigeria.  
Recipient must obtain the written authority of the said company before wholly or partially duplicating.  
All rights reserved.

|   |   |   |
|---|---|---|
| DRAWN: A.HAMALI<br>DATE: 17MAY24<br>CHECKED: O.SAHEED<br>DATE: 17MAY24<br>APPROVED: K.HARUNA<br>DATE: 17MAY24<br>APPD. LING: |  <b>NIGERIA LIQUEFIED NATURAL GAS</b><br>PROJECT:<br>NEW LIQ WAREHOUSE PROJECT<br>LOCATION:<br>NLNG INDUSTRIAL AREA BONNY ISLAND<br>TITLE:<br>FOUNDATIONS DRAWING – GENERAL<br>FOUNDATION AND SECTIONS |  DISCIPLINE: CIVIL<br>UNIT NO: 8490 |
| DATE: CONTRACT C.O. DWG. No.                                                                                                 | SCALE: 1:100, U.N.O<br>NLNG PROJECT No. 19/MOC/PDR/014P<br>DRAWING No. B-67.366<br>SHEET 1 OF 2<br>REV A   |   |



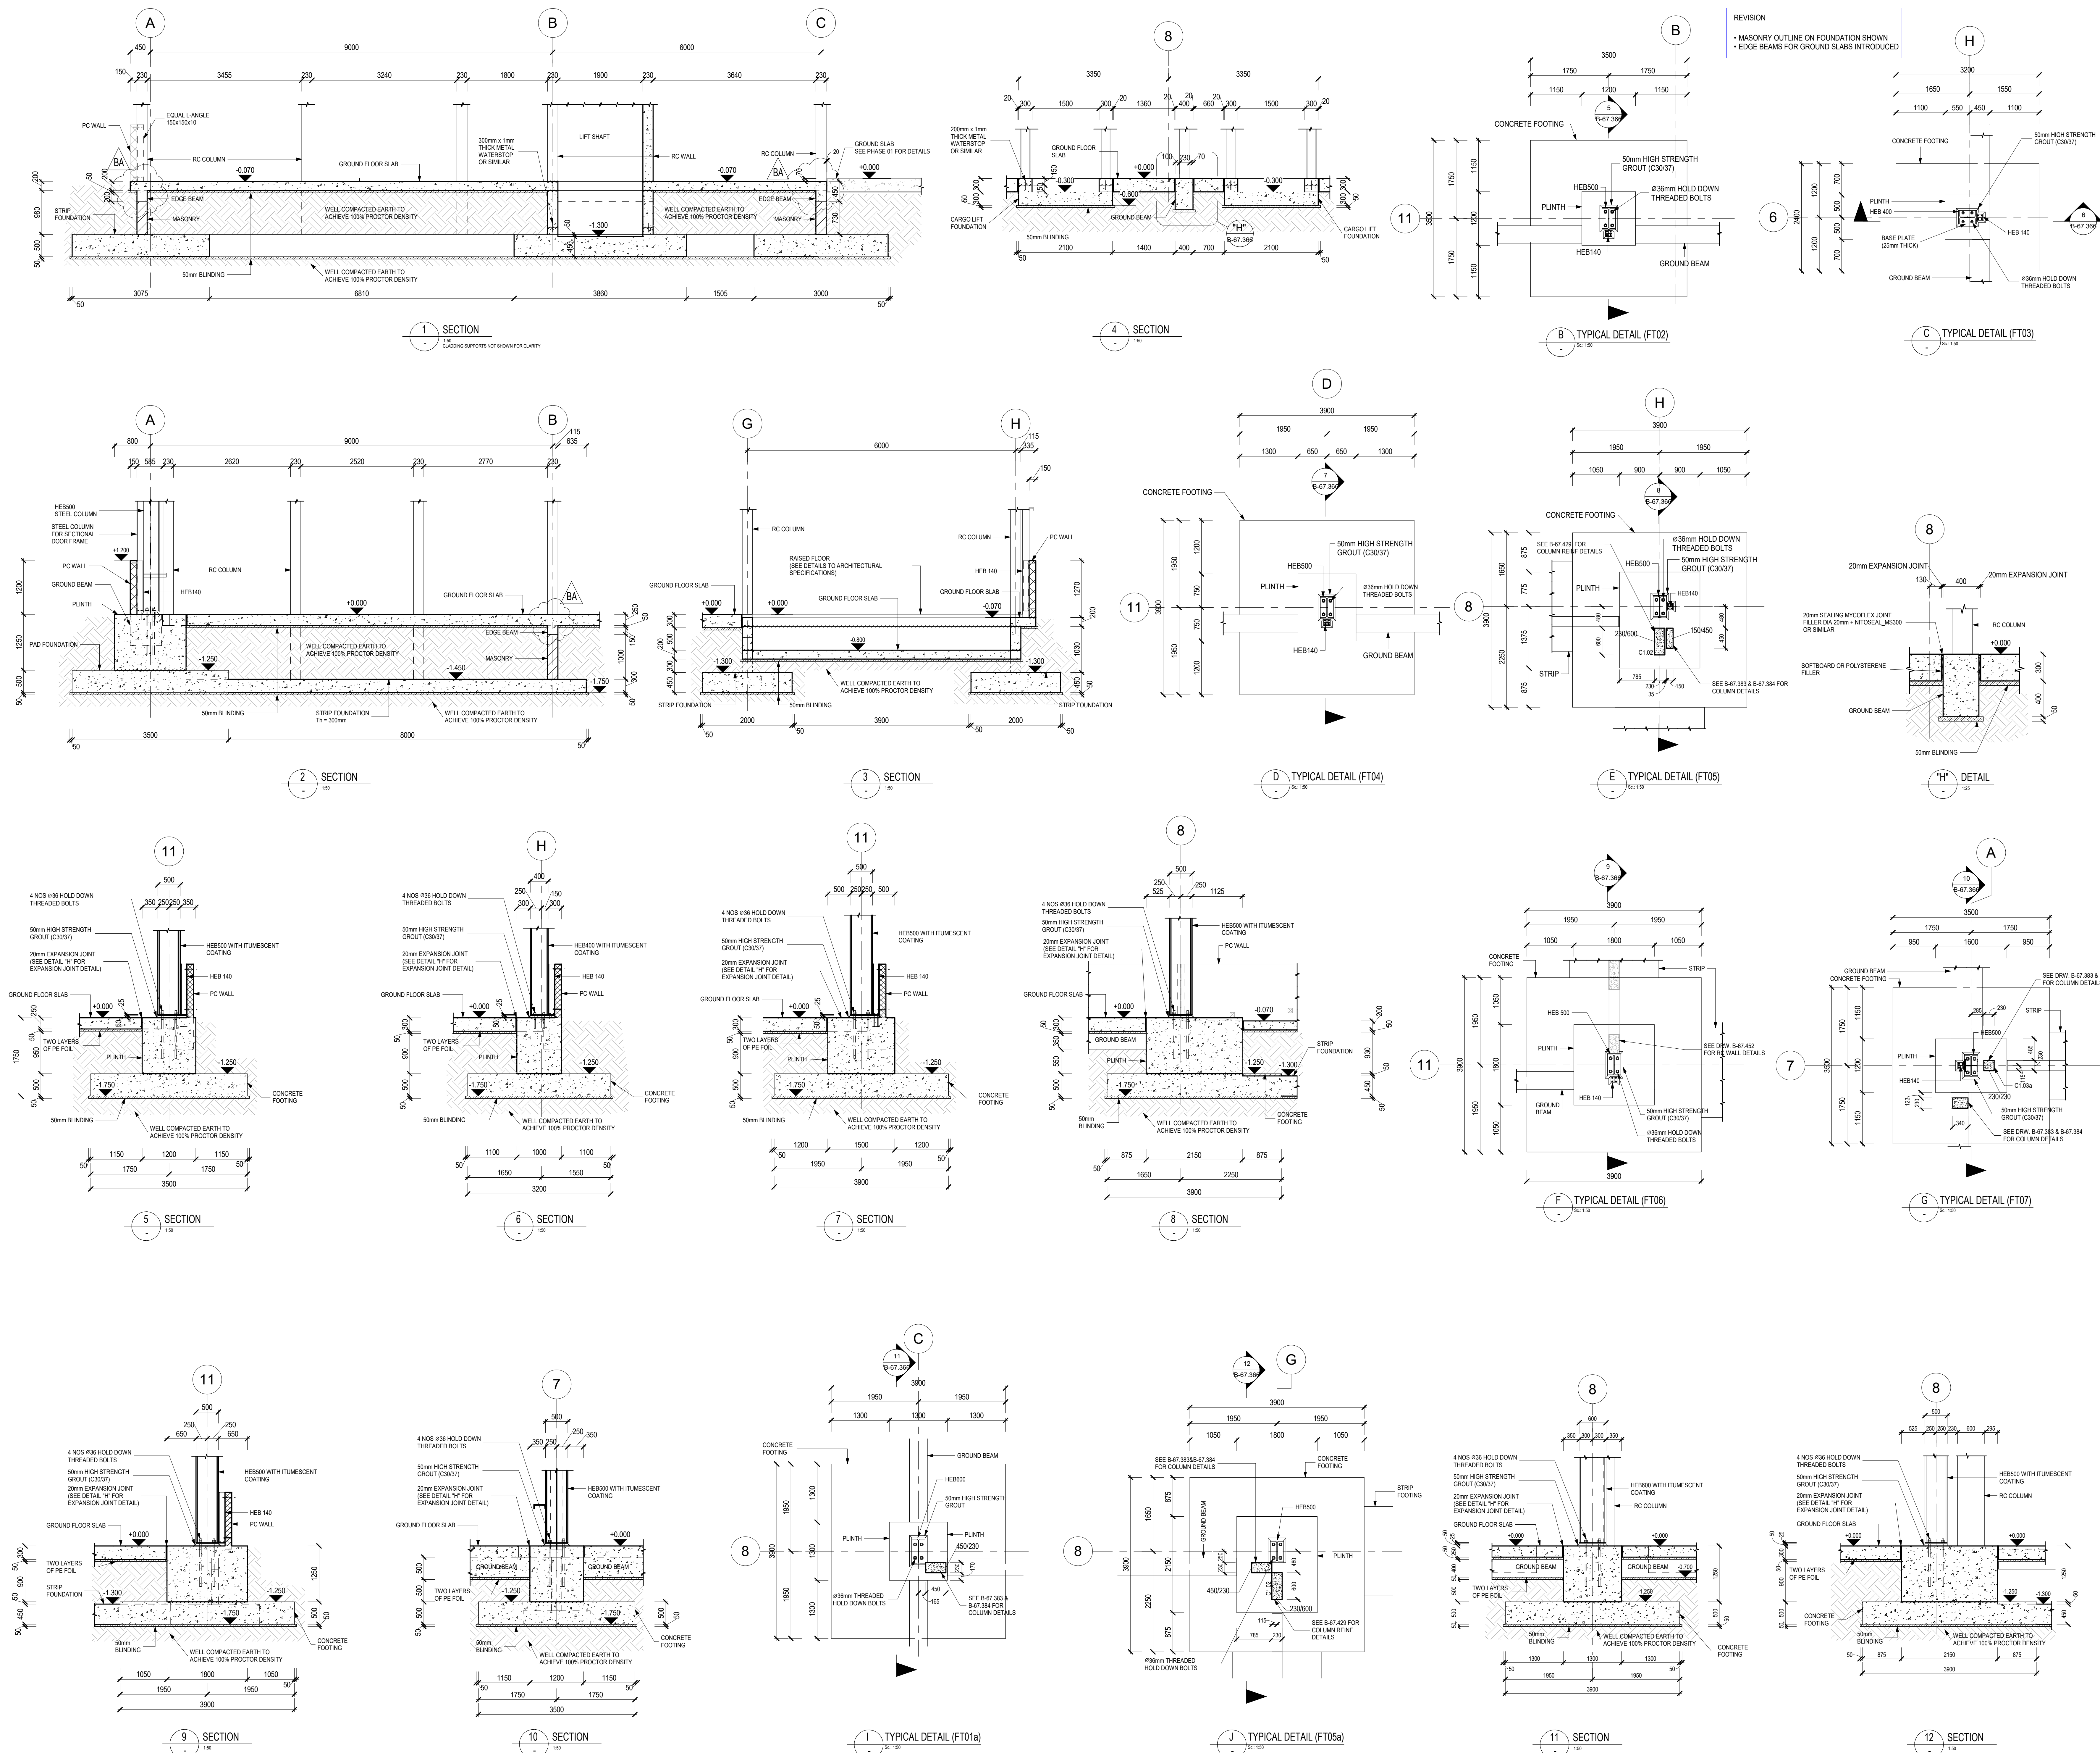

- NOTES
1. ALL DIMENSIONS ARE IN MILLIMETERS (mm) AND LEVELS IN METERS.
  2. ALL LEVELS, REFER TO DATUM LINE = 0.000
  3. UNO - UNLESS NOTED OTHERWISE, X - CONNECTION DETAIL TAG, C - COLUMN, FT - FOOTING TYPE: PC - PRECAST.
  4. REFER TO M-E DRAWINGS FOR ALL CONDUIT PIPES, BEAM AND WALL OPENINGS.

ALL STEELWORKS DIMENSIONS AND DETAILS SHALL BE READ FROM THE DRAWINGS LISTED BELOW

FOR DETAILED STEELWORKS CONNECTIONS AND SPECIFICATIONS, KINDLY REFER TO THE FOLLOWING DRAWINGS:

- B-67.386
- B-67.387
- B-67.389
- B-67.406
- B-67.407
- B-67.408
- B-67.409
- B-67.410
- B-67.411
- B-67.412
- B-67.413
- B-67.416
- B-67.417
- B-67.418
- B-67.419

#### LEGEND

|  |                                  |  |                       |
|--|----------------------------------|--|-----------------------|
|  | NEW CONCRETE                     |  | TOP OF CONCRETE       |
|  | PRECAST CONCRETE                 |  | TOP OF FINISH. CONCR. |
|  | LEAN CONCRETE                    |  | TOP OF CONCRETE       |
|  | CONCR. TO BE CAST LATER          |  | TOP OF FINISH. CONCR. |
|  | MASONRY                          |  | CONSTRUCTION JOINT    |
|  | CONCRETE MASONRY                 |  | ANCHORING RAILS       |
|  | SAND FILL OR MORTAR SETTING BED  |  | EARTH WIRE            |
|  | OPENINGS IN WALLS                |  | STRIP STEEL           |
|  | OPENINGS IN SLABS                |  | 30x5 BUILT IN PARTS   |
|  | BAR GRATING                      |  | TL TOP LEVEL          |
|  | CHECKED PLATE                    |  | BSL BOTTOM LEVEL      |
|  | BOX FOR REINFORCEMENT CONNECTION |  | WSL WALL SLOT         |
|  | DETAIL FOR CONCRETE EDGES        |  | FOP FLOOR OPENING     |
|  | WORKING JOINT                    |  | COP CEILING OPENING   |
|  | CONTRACTION JOINT                |  | WOP WALL OPENING      |
|  |                                  |  | IL INVERT LEVEL       |
|  |                                  |  | CL CENTER LINE        |


HMS 25/15 HMS 25/15 GENERALLY AT ALL CONNECTIONS BETWEEN CONCRETE AND BRICKWORK SEE ALSO ARCHITECTURAL DRAWING

| EXPOSED CONCRETE GENERALLY (WITHOUT FOUNDATIONS) |                   |                        |                     |
|--------------------------------------------------|-------------------|------------------------|---------------------|
| STRUCTURAL COMPONENT                             | CLASS OF CONCRETE | GRADE OF REINFORCEMENT | NOMINAL COVER $c_n$ |
| FOOTING (TOP/BTM)                                | C25/30            | B500B                  | 40mm                |
| GROUND SLAB                                      | C25/30            | B500B                  | 40mm                |
| GROUND BEAM                                      | C25/30            | B500B                  | 40mm                |
| PLINTH                                           | C25/30            | B500B                  | 40mm                |

#### REFERENCE TO DRAWINGS

| DRAWING-NO. | TITLE                                                  |
|-------------|--------------------------------------------------------|
| B-67.367    | GROUND FLOOR AND SECTIONS                              |
| B-67.311    | NEW IA WAREHOUSE - FOUNDATION LAYOUT - RACKING STORAGE |
| B-67.301    | GROUND FLOOR LAYOUT                                    |
| B-67.261    | SITE FINISHED LEVELS LAYOUT                            |
| B-67.373    | PAD FOUNDATION REINFORCEMENT                           |
| B-67.375    | GROUND BEAMS REINFORCEMENT                             |
| B-67.383    | MASONRY WALL FRAMING                                   |
| B-67.384    | MASONRY WALL FRAMING                                   |
| B-67.452    | WALLS AROUND STAIRCASE 3 REINFORCEMENT                 |

DATUM LINE =  $\pm 0.00m$  (FFL) = 3.5m

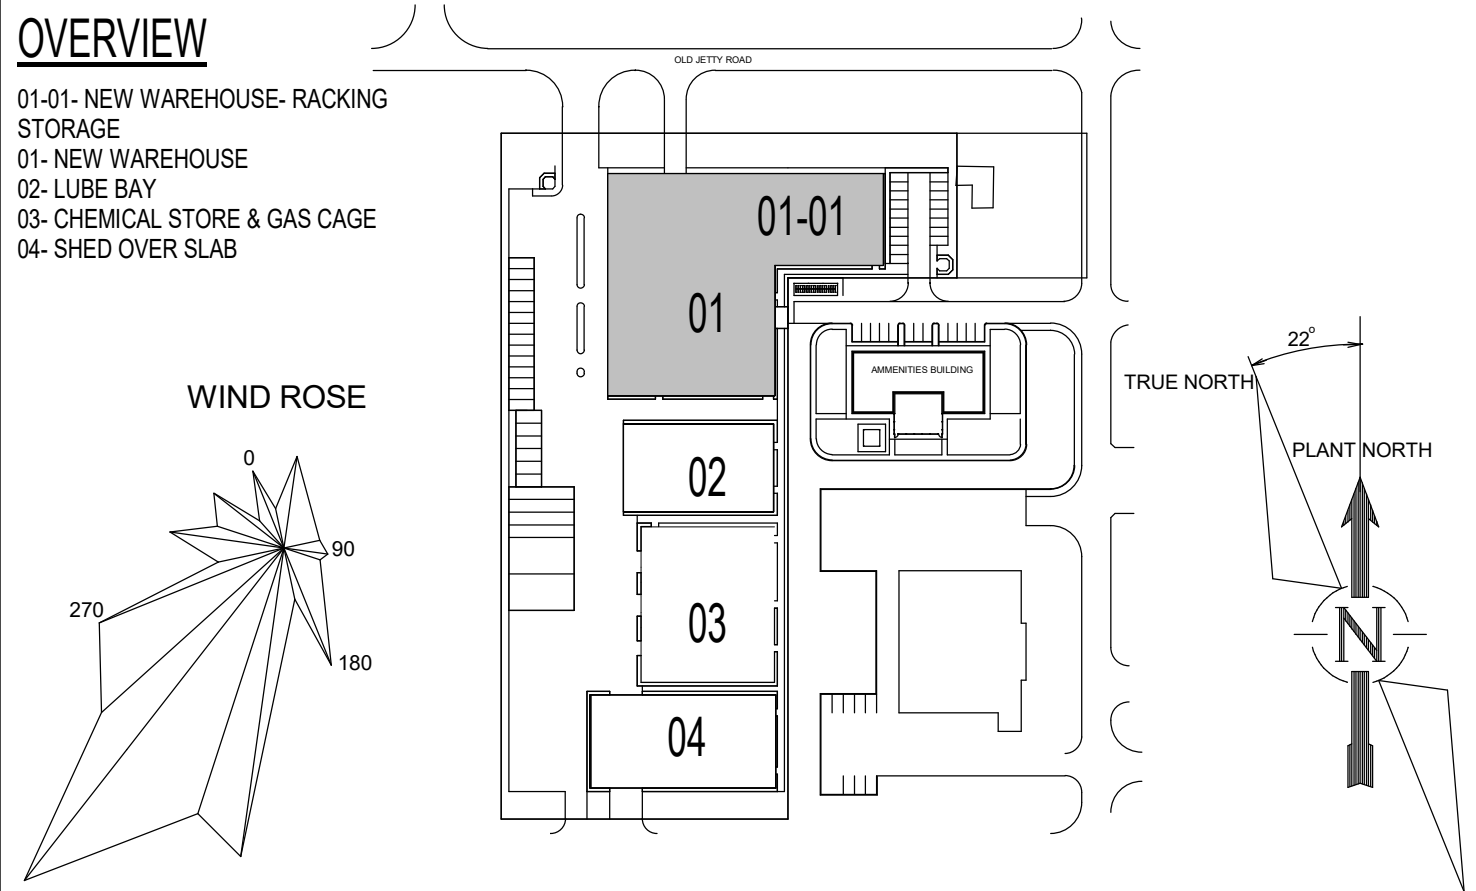

| REV | DESCRIPTION               | DATE    | CHKD | DATE    | APPD | DATE    |
|-----|---------------------------|---------|------|---------|------|---------|
| BA  | AFC UPDATED               | 27NOV24 | OS   | 27NOV24 | KH   | 27NOV24 |
| B   | APPROVED FOR CONSTRUCTION | 31OCT24 | OS   | 31OCT24 | KH   | 31OCT24 |
| A   | ISSUED FOR APPROVAL       | 10SEP24 | OS   | 10SEP24 | KH   | 10SEP24 |
| O   | ISSUED FOR COMMENT        | 17MAY24 | OS   | 17MAY24 | KH   | 17MAY24 |
| REV | DESCRIPTION               | DWN     | DATE | CHKD    | DATE | APPD    |

| REVISIONS   |                                             |                   |                      |                                      |                         |           |
|---|---------------------------------------------|-------------------|----------------------|--------------------------------------|-------------------------|-----------|
| This Document is confidential. The copyright therein is vested in Nigeria LNG Ltd, Nigeria. Recipient must obtain the written authority of the said company before wholly or partially duplicating. All rights reserved. |                                             |                   |                      |                                      |                         |           |
| DRAWING: A.HAMBALI   | DATE: 17MAY24                               | CHECKED: O.SAHEED | DATE: 17MAY24        | APPROVED: K.HARUNA                   | DATE: 17MAY24           | APPD: LNC |
| PROJECT: NEW IA WAREHOUSE   | LOCATION: NLNG INDUSTRIAL AREA BONNY ISLAND | DISCIPLINE: CIVIL | UNIT No: 8490        | TITLE: FOUNDATIONS DRAWING - GENERAL |                         |           |
| CONTRACT CO. DWG. No. 0100210001   | NLNG PROJECT No. 19/MOC/PDR/014P            |                   | DRAWING No. B-67.366 |                                      | FOUNDATION AND SECTIONS |           |
| SCALE: 1:50, U.N.O.   |                                             |                   |                      |                                      | SHEET 2 OF 2            | REV BA    |

CADREF: B-67.366-SH2-BA

ORIGINAL SIZE: A0

CLASSIFICATION: MOST CONFIDENTIAL

CONFIDENTIAL

RESTRICTED

UNRESTRICTED