


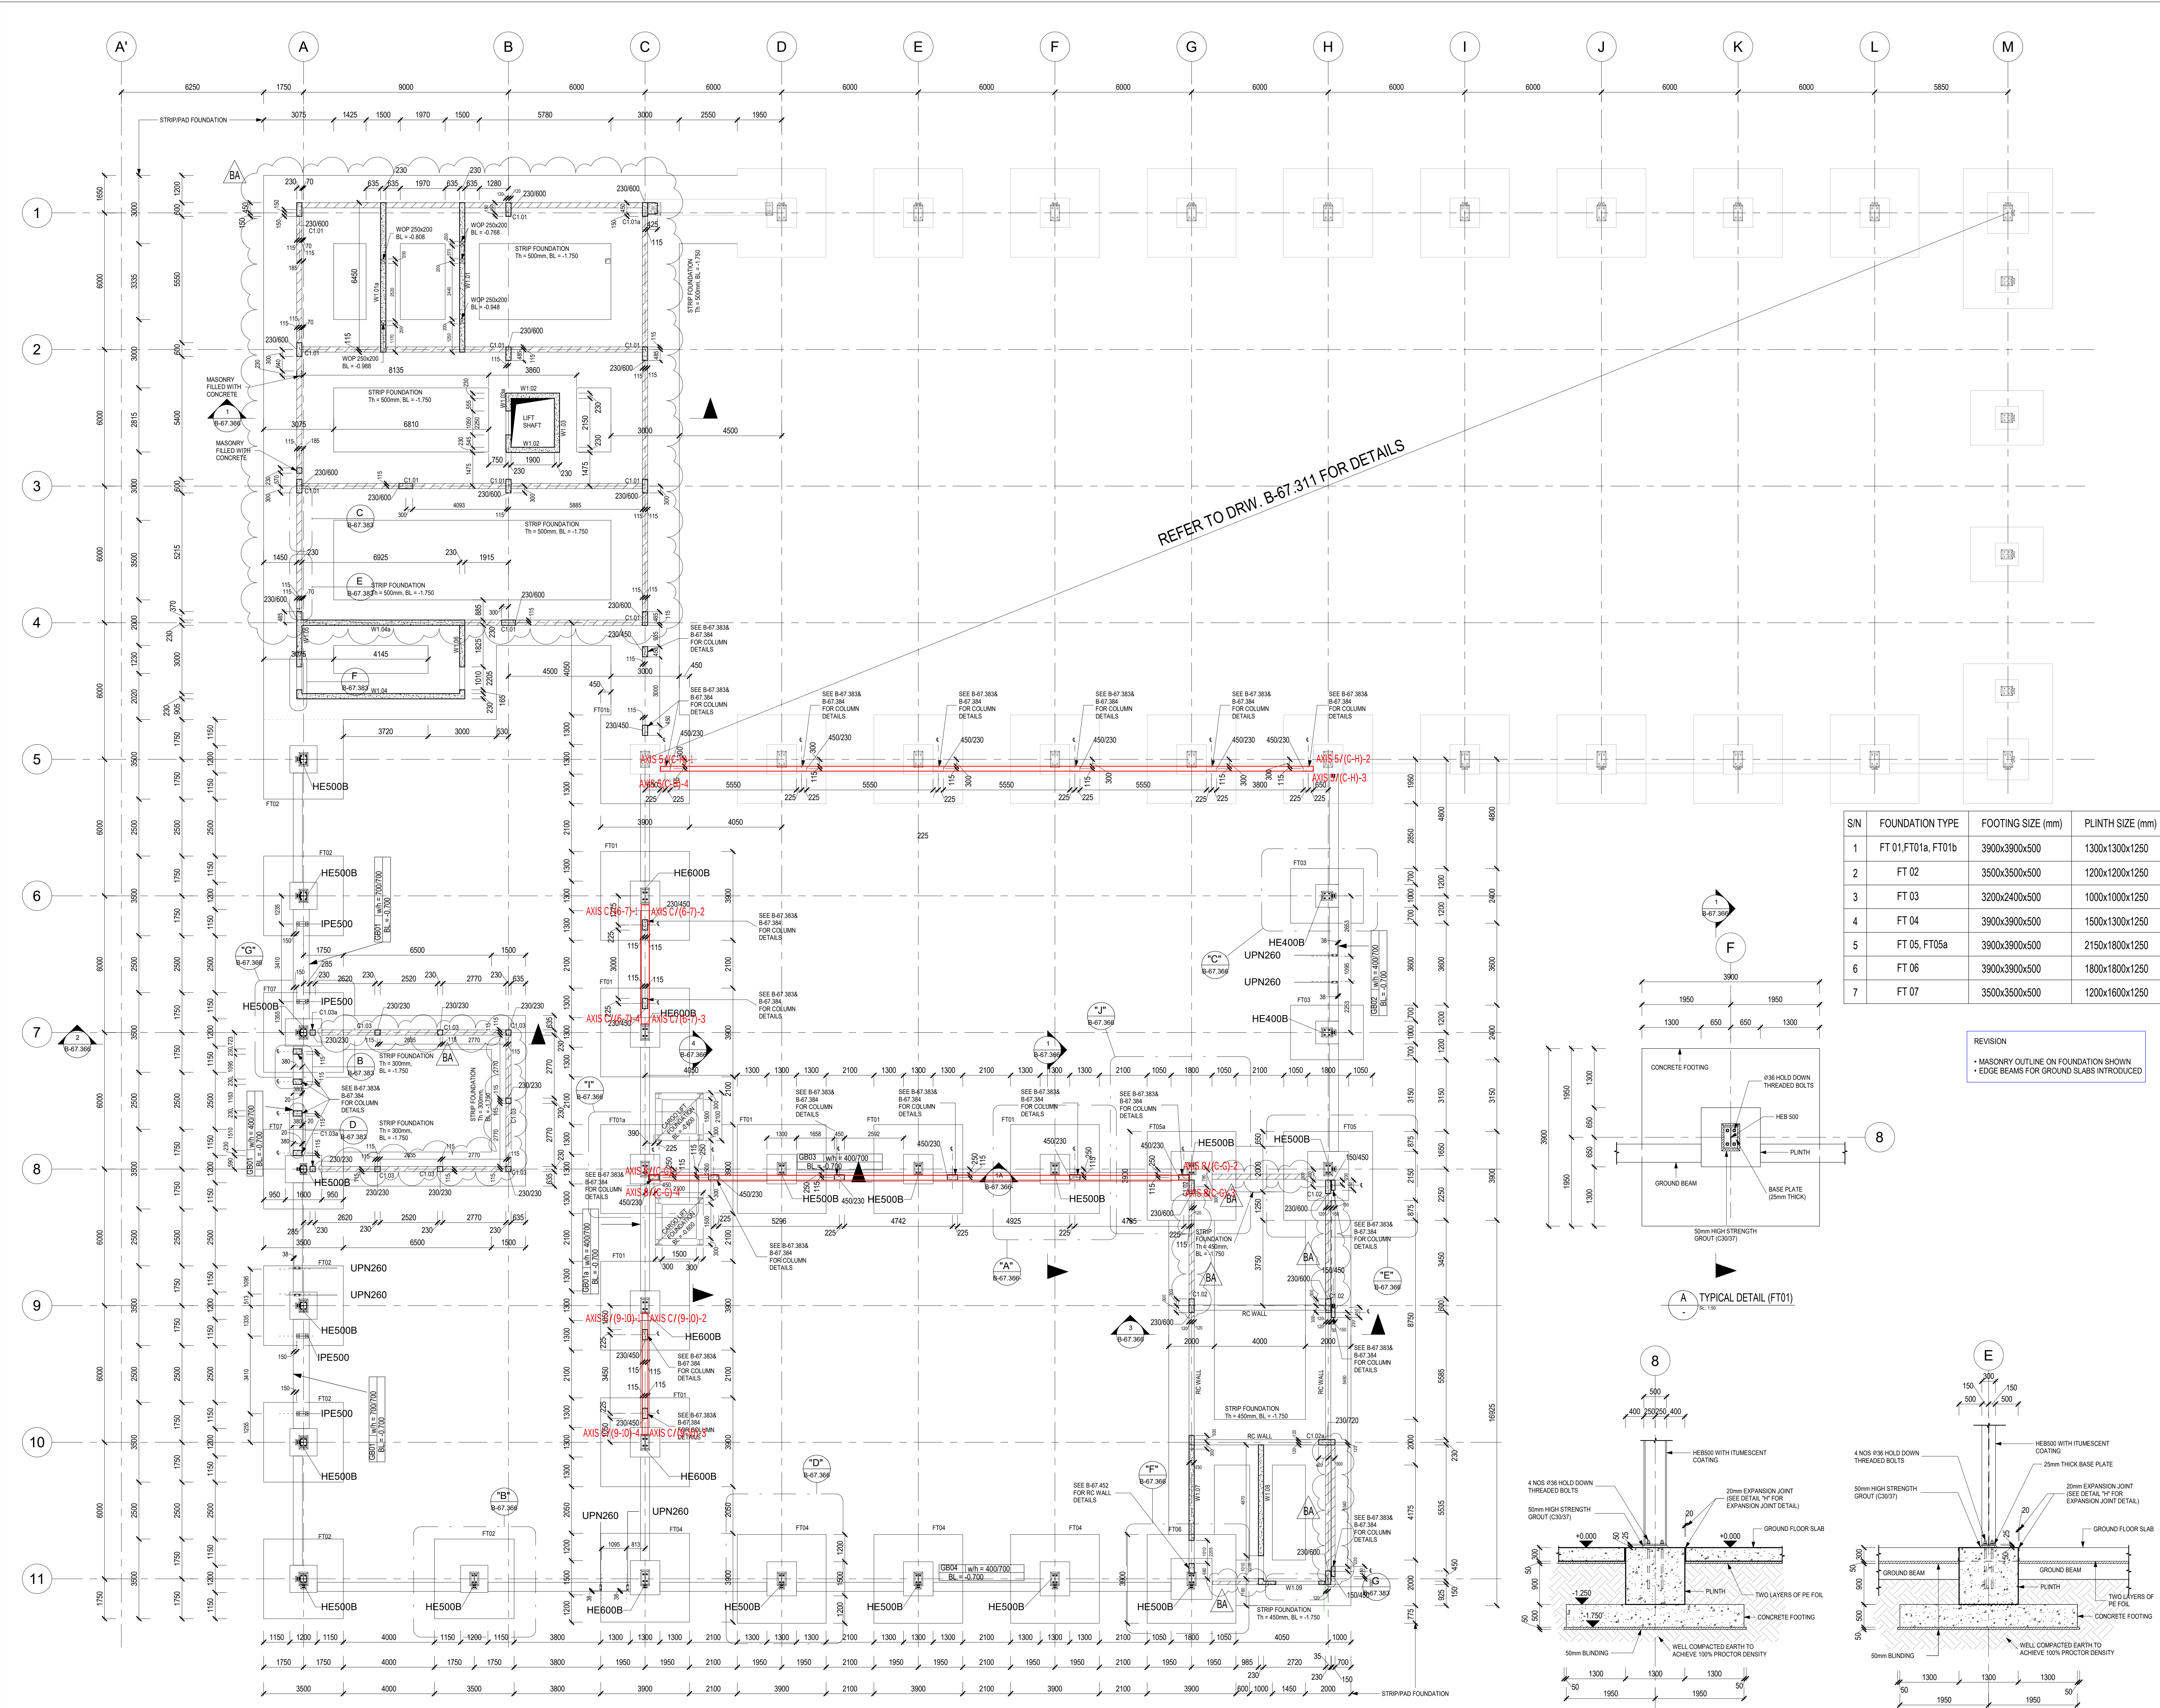

NOTES

- ALL DIMENSIONS ARE IN MILLIMETERS (mm) AND LEVELS IN METERS.
- ALL LEVELS, REFER TO DATUM LINE = 0.00
- UNO - UNLESS NOTED OTHERWISE, X - CONNECTION DETAIL TAG, C - COLUMN, FT - FOOTING TYPE, PC - PRECAST.
- REFER TO M-E DRAWINGS FOR ALL CONDUIT PIPES, BEAM AND WALL OPENINGS.

ALL STEELWORKS DIMENSIONS AND DETAILS SHALL BE READ FROM THE DRAWINGS LISTED BELOW

FOR DETAILED STEELWORKS CONNECTIONS AND SPECIFICATIONS, KINDLY REFER TO THE FOLLOWING DRAWINGS:

- B-67.386
- B-67.387
- B-67.389
- B-67.406
- B-67.407
- B-67.408
- B-67.409
- B-67.410
- B-67.412
- B-67.413
- B-67.416
- B-67.417
- B-67.418
- B-67.419

LEGEND

	NEW CONCRETE		TOP OF CONCRETE
	PRECAST CONCRETE		TOP OF FINISH. CONCR.
	LEAN CONCRETE		TOP OF CONCRETE
	CONCR. TO BE CAST LATER		TOP OF FINISH. CONCR.
	MASONRY		CONSTRUCTION JOINT
	CONCRETE MASONRY		ANCHORING RAILS
	SAND FILL OR MORTAR SETTING BED		EARTH WIRE
	OPENINGS IN WALLS		STRIP STEEL
	OPENINGS IN SLABS		BUILTS IN PARTS
	BAR GRATING		TOP LEVEL
	CHECKED PLATE		BOTTOM LEVEL
	BOX FOR REINFORCEMENT CONNECTION		WALL SLOT
	DETAIL FOR CONCRETE EDGES		FLOOR OPENING
	WORKING JOINT		CEILING OPENING
	CONTRACTION JOINT		WALL OPENING
			INVERT LEVEL
			CENTER LINE

S/N	FOUNDATION TYPE	FOOTING SIZE (mm)	PLINTH SIZE (mm)
1	FT 01, FT01a, FT01b	3900x3900x500	1300x1300x1250
2	FT 02	3500x3500x500	1200x1200x1250
3	FT 03	3200x2400x500	1000x1000x1250
4	FT 04	3900x3900x500	1500x1300x1250
5	FT 05, FT05a	3900x3900x500	2150x1800x1250
6	FT 06	3900x3900x500	1800x1800x1250
7	FT 07	3500x3500x500	1200x1600x1250

REVISION

- MASONRY OUTLINE ON FOUNDATION SHOWN
- EDGE BEAMS FOR GROUND SLABS INTRODUCED

TYPICAL DETAIL (FT01)

SECTION 1

SECTION 1A

DATUM LINE = ±0.00m (FFL) = 3.5m

OVERVIEW

01-01: NEW WAREHOUSE - RACKING STORAGE
01-02: NEW WAREHOUSE
02-03: LUBE BAY
03-04: CHEMICAL STORE & GAS CAGE
04-05: SHED OVER STAIR


REV	DESCRIPTION	DWN	DATE	CHKD	DATE	APPD	DATE
BA	AFC UPDATED	AH	27NOV24	OS	27NOV24	KH	27NOV24
B	APPROVED FOR CONSTRUCTION	AH	06NOV24	OS	06NOV24	KH	06NOV24
A	ISSUED FOR APPROVAL	AH	10SEP24	OS	10SEP24	KH	10SEP24
O	ISSUED FOR COMMENT	AH	17MAY24	OS	17MAY24	KH	17MAY24

This Document is confidential. The copyright therein is vested in Nigeria LNG Ltd, Nigeria. Recipient must obtain the written authority of the said company before wholly or partially duplicating. All rights reserved.

DRAWING: A.HAMBA
DATE: 17MAY24
CHECKED: O.SAHEED
DATE: 17MAY24
APPROVED: K.HARUNA
DATE: 17MAY24
APPD. LNG:
CONTRACT CO. DWG. No.
FOUNDATION AND SECTIONS

SCALE: 1:100, U.N.O. 19/MOC/PDR/014P

NIGERIA LIQUEFIED NATURAL GAS
PROJECT: NEW TA WAREHOUSE PROJECT
LOCATION: NLNG INDUSTRIAL AREA BONNY ISLAND
DISCIPLINE: CIVIL
UNIT No: 8490
TITLE: FOUNDATIONS DRAWING - GENERAL
SHEET: 1 OF 2
REV: BA

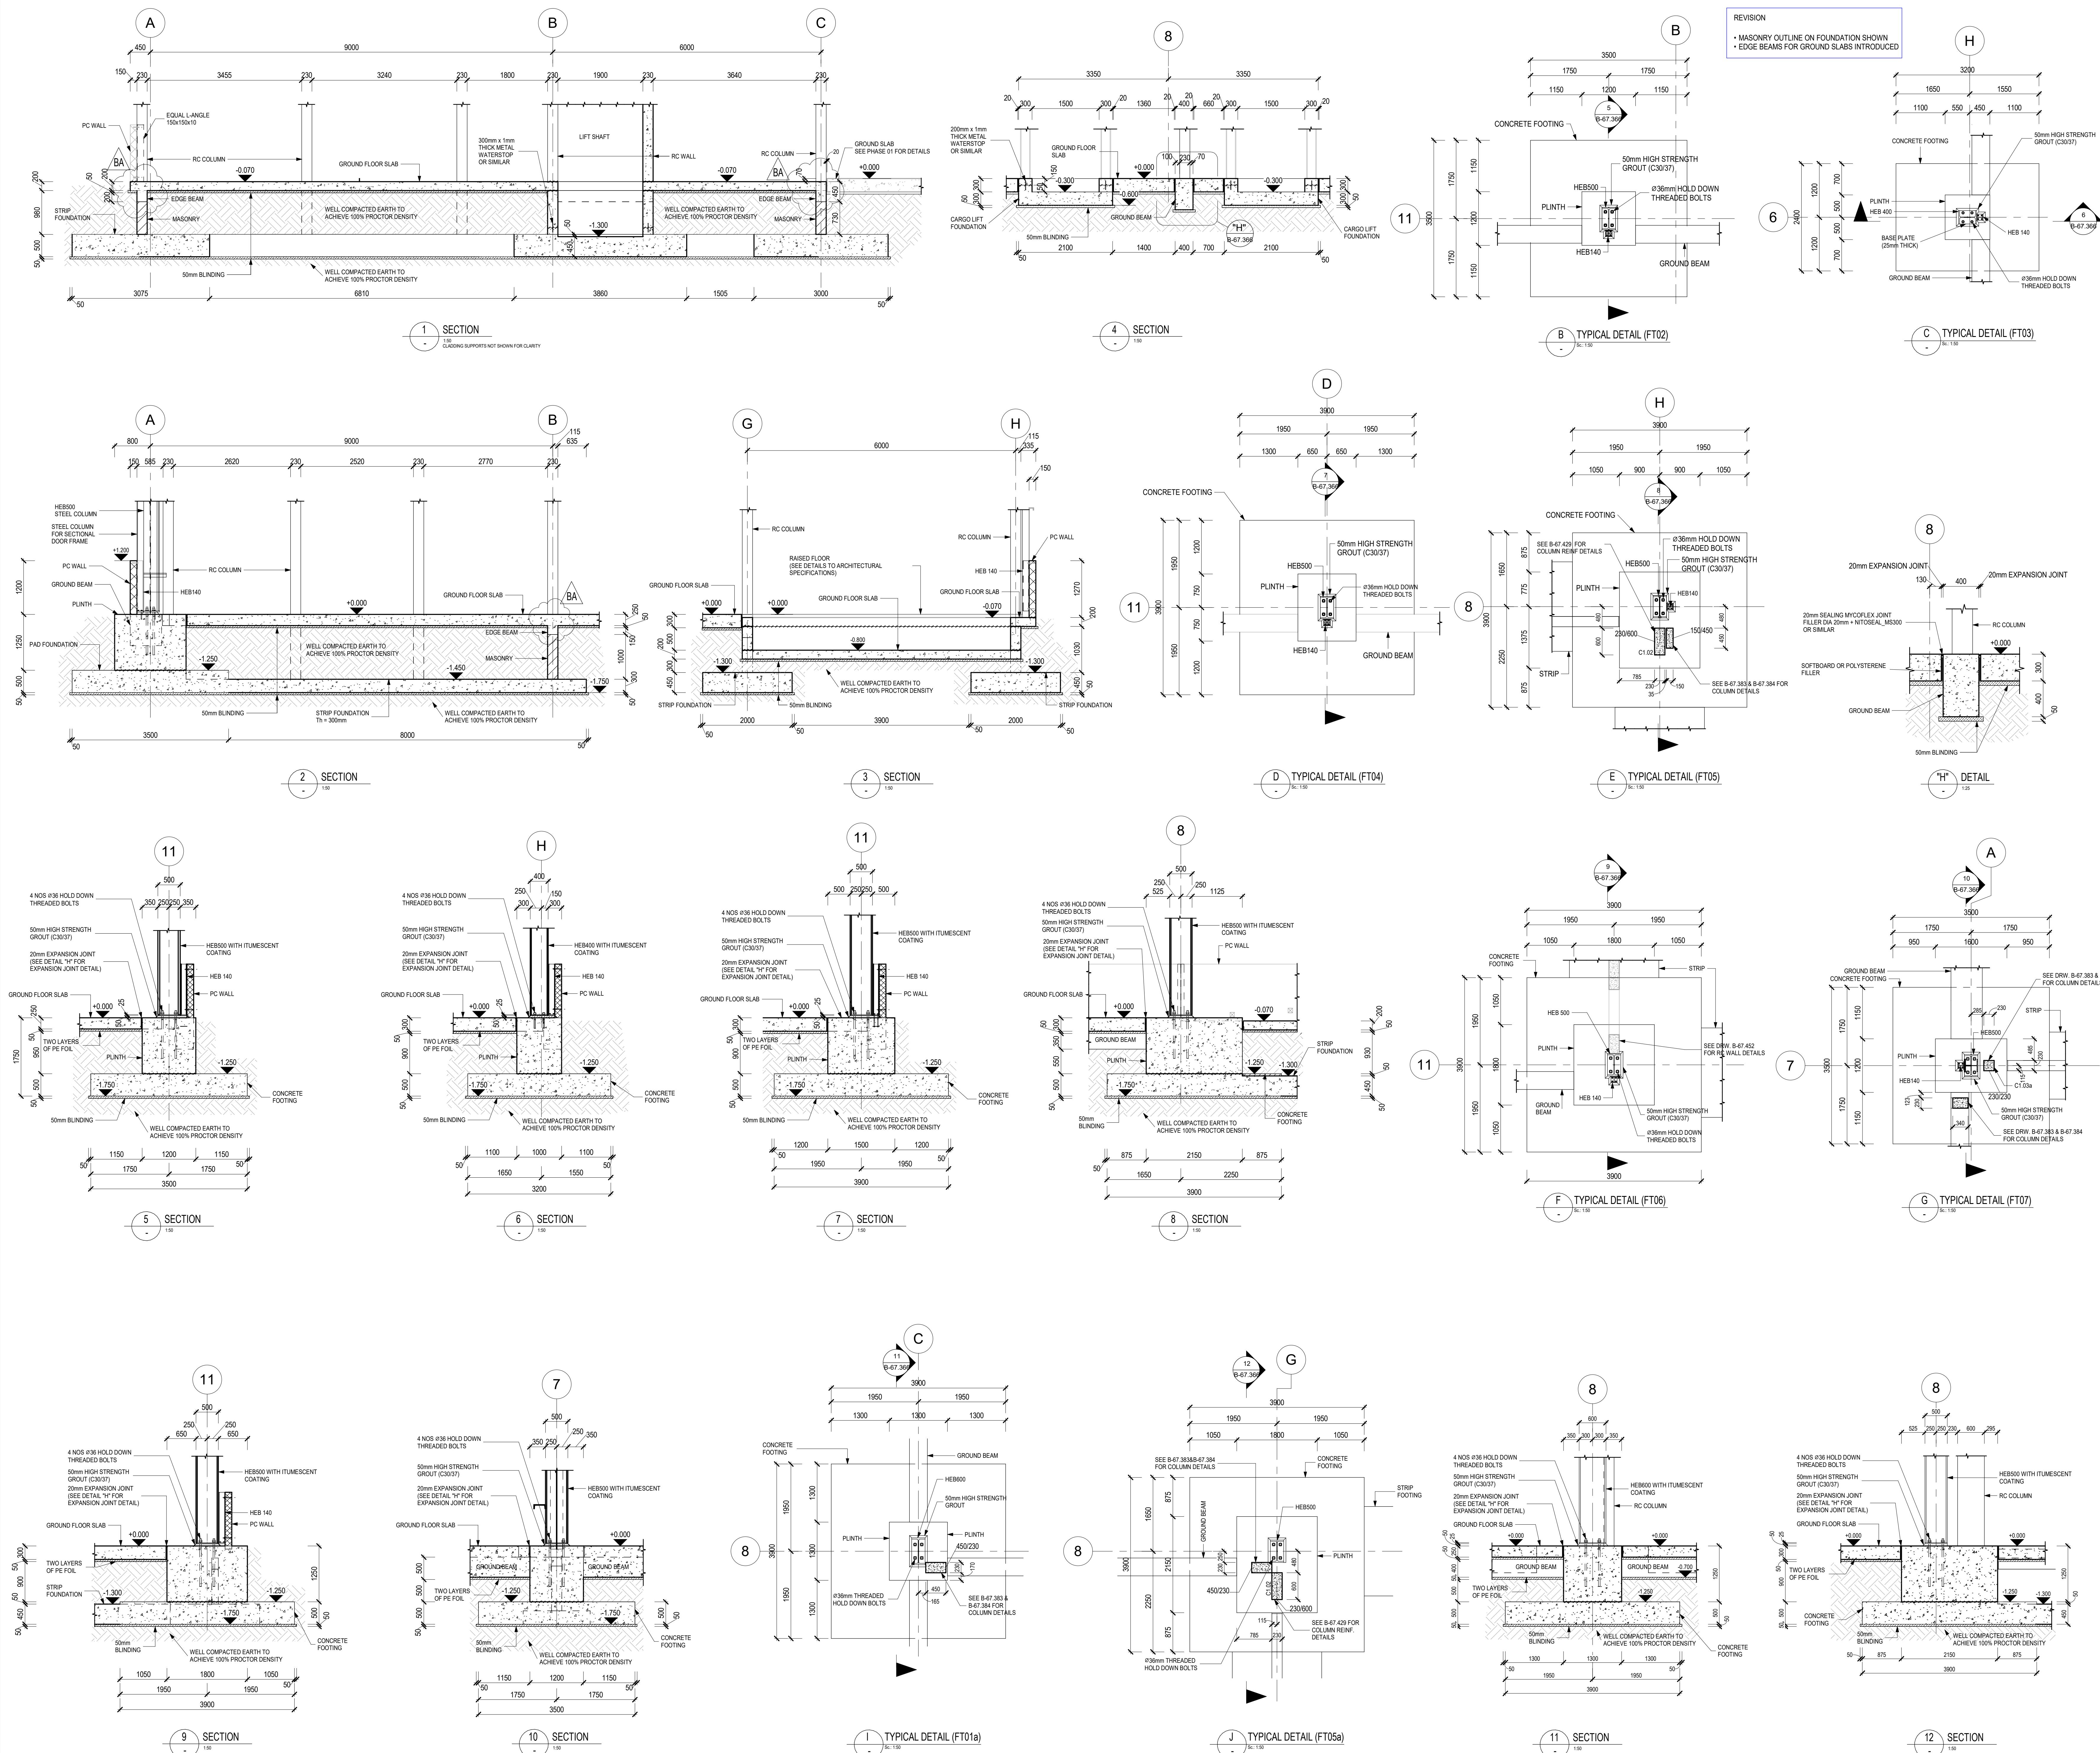

- NOTES
1. ALL DIMENSIONS ARE IN MILLIMETERS (mm) AND LEVELS IN METERS.
 2. ALL LEVELS, REFER TO DATUM LINE = 0.000
 3. UNO - UNLESS NOTED OTHERWISE, X - CONNECTION DETAIL TAG, C - COLUMN, FT - FOOTING TYPE: PC - PRECAST.
 4. REFER TO M-E DRAWINGS FOR ALL CONDUIT PIPES, BEAM AND WALL OPENINGS.

ALL STEELWORKS DIMENSIONS AND DETAILS SHALL BE READ FROM THE DRAWINGS LISTED BELOW

FOR DETAILED STEELWORKS CONNECTIONS AND SPECIFICATIONS, KINDLY REFER TO THE FOLLOWING DRAWINGS:

- B-67.386
- B-67.387
- B-67.389
- B-67.406
- B-67.407
- B-67.408
- B-67.409
- B-67.410
- B-67.411
- B-67.412
- B-67.413
- B-67.416
- B-67.417
- B-67.418
- B-67.419

LEGEND

	NEW CONCRETE		TOP OF CONCRETE
	PRECAST CONCRETE		TOP OF FINISH. CONCR.
	LEAN CONCRETE		TOP OF CONCRETE
	CONCR. TO BE CAST LATER		TOP OF FINISH. CONCR.
	MASONRY		CONSTRUCTION JOINT
	CONCRETE MASONRY		ANCHORING RAILS
	SAND FILL OR MORTAR SETTING BED		EARTH WIRE
	OPENINGS IN WALLS		STRIP STEEL
	OPENINGS IN SLABS		30x5 BUILT IN PARTS
	BAR GRATING		TL TOP LEVEL
	CHECKED PLATE		BSL BOTTOM LEVEL
	BOX FOR REINFORCEMENT CONNECTION		WSL WALL SLOT
	DETAIL FOR CONCRETE EDGES		FOP FLOOR OPENING
	WORKING JOINT		COP CEILING OPENING
	CONTRACTION JOINT		WOP WALL OPENING
			IL INVERT LEVEL
			CL CENTER LINE


HMS 25/15 HMS 25/15 GENERALLY AT ALL CONNECTIONS BETWEEN CONCRETE AND BRICKWORK SEE ALSO ARCHITECTURAL DRAWING

EXPOSED CONCRETE GENERALLY (WITHOUT FOUNDATIONS)			
STRUCTURAL COMPONENT	CLASS OF CONCRETE	GRADE OF REINFORCEMENT	NOMINAL COVER c_n
FOOTING (TOP/BTM)	C25/30	B500B	40mm
GROUND SLAB	C25/30	B500B	40mm
GROUND BEAM	C25/30	B500B	40mm
PLINTH	C25/30	B500B	40mm

REFERENCE TO DRAWINGS

DRAWING-NO.	TITLE
B-67.367	GROUND FLOOR AND SECTIONS
B-67.311	NEW IA WAREHOUSE - FOUNDATION LAYOUT - RACKING STORAGE
B-67.301	GROUND FLOOR LAYOUT
B-67.261	SITE FINISHED LEVELS LAYOUT
B-67.373	PAD FOUNDATION REINFORCEMENT
B-67.375	GROUND BEAMS REINFORCEMENT
B-67.383	MASONRY WALL FRAMING
B-67.384	MASONRY WALL FRAMING
B-67.452	WALLS AROUND STAIRCASE 3 REINFORCEMENT

DATUM LINE = $\pm 0.00m$ (FFL) = 3.5m

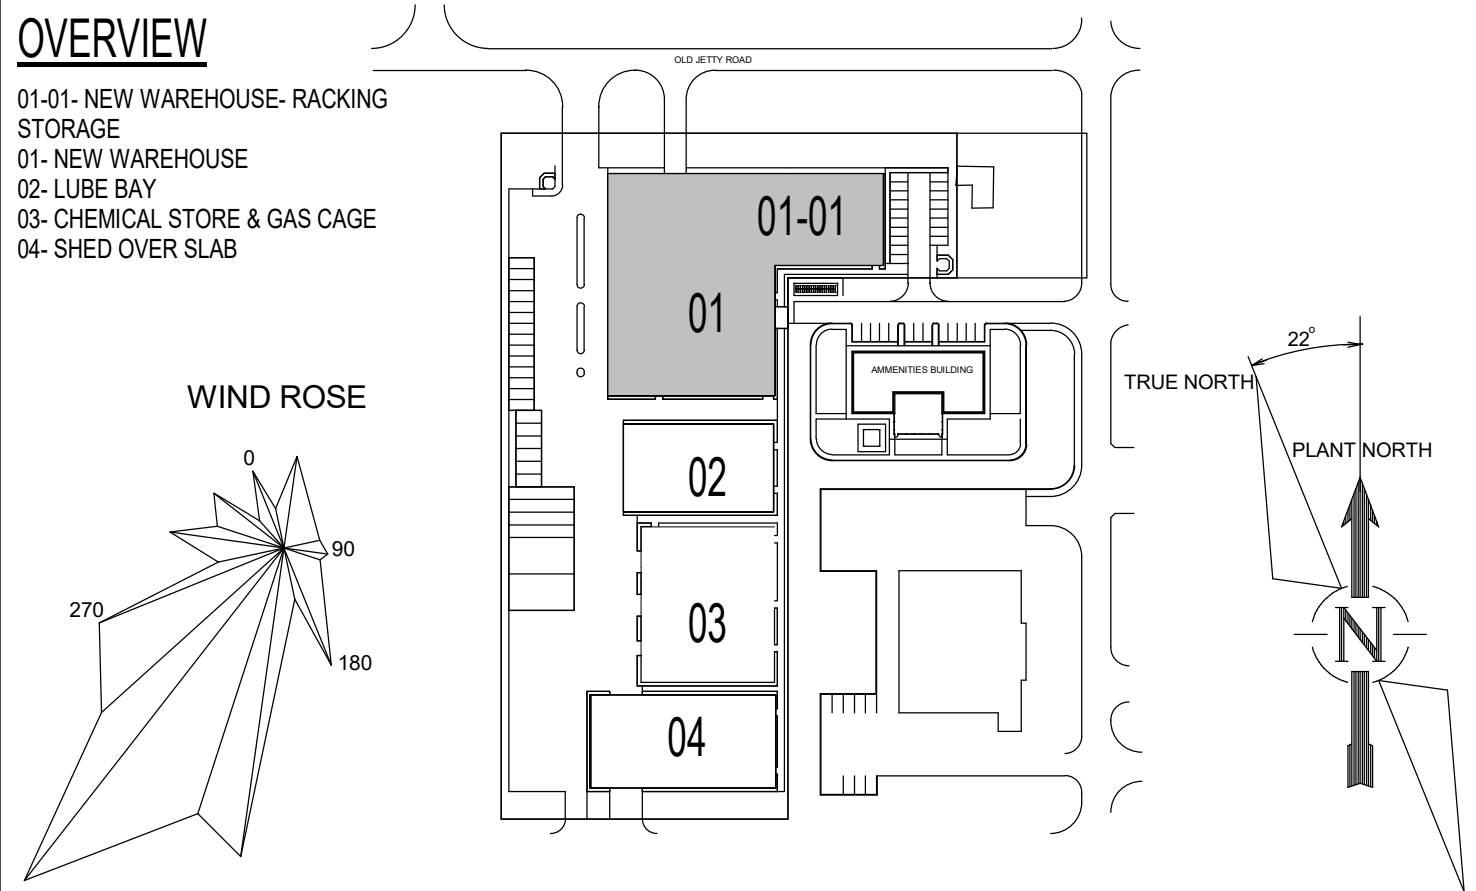

REV	DESCRIPTION	DATE	CHKD	DATE	APPD	DATE
BA	AFC UPDATED	27NOV24	OS	27NOV24	KH	27NOV24
B	APPROVED FOR CONSTRUCTION	31OCT24	OS	31OCT24	KH	31OCT24
A	ISSUED FOR APPROVAL	10SEP24	OS	10SEP24	KH	10SEP24
O	ISSUED FOR COMMENT	17MAY24	OS	17MAY24	KH	17MAY24
REV	DESCRIPTION	DWN	DATE	CHKD	DATE	APPD

REVISIONS					
This Document is confidential. The copyright therein is vested in Nigeria LNG Ltd, Nigeria. Recipient must obtain the written authority of the said company before wholly or partially duplicating. All rights reserved.					
DRAWING: A.HAMBALI	DATE: 17MAY24	CHECKED: O.SAHEED	DATE: 17MAY24	APPROVED: K.HARUNA	DATE: 17MAY24
CONTRACT CO. DWG. No. 0100210001	LOCATION NLNG INDUSTRIAL AREA BONNY ISLAND	DISCIPLINE CIVIL	UNIT No. 8490	TITLE FOUNDATIONS DRAWING - GENERAL	
SCALE 1:50, U.N.O.	NLNG PROJECT No. 19/MOC/PDR/014P	DRAWING No. B-67.366	SHEET 2 OF 2	REV BA	

CADREF: B-67.366-SH2-BA

ORIGINAL SIZE: A0

CLASSIFICATION: MOST CONFIDENTIAL

CONFIDENTIAL

RESTRICTED

UNRESTRICTED