


GRADE SLAB FORMWORK PLAN - A

1:100

AB.F3

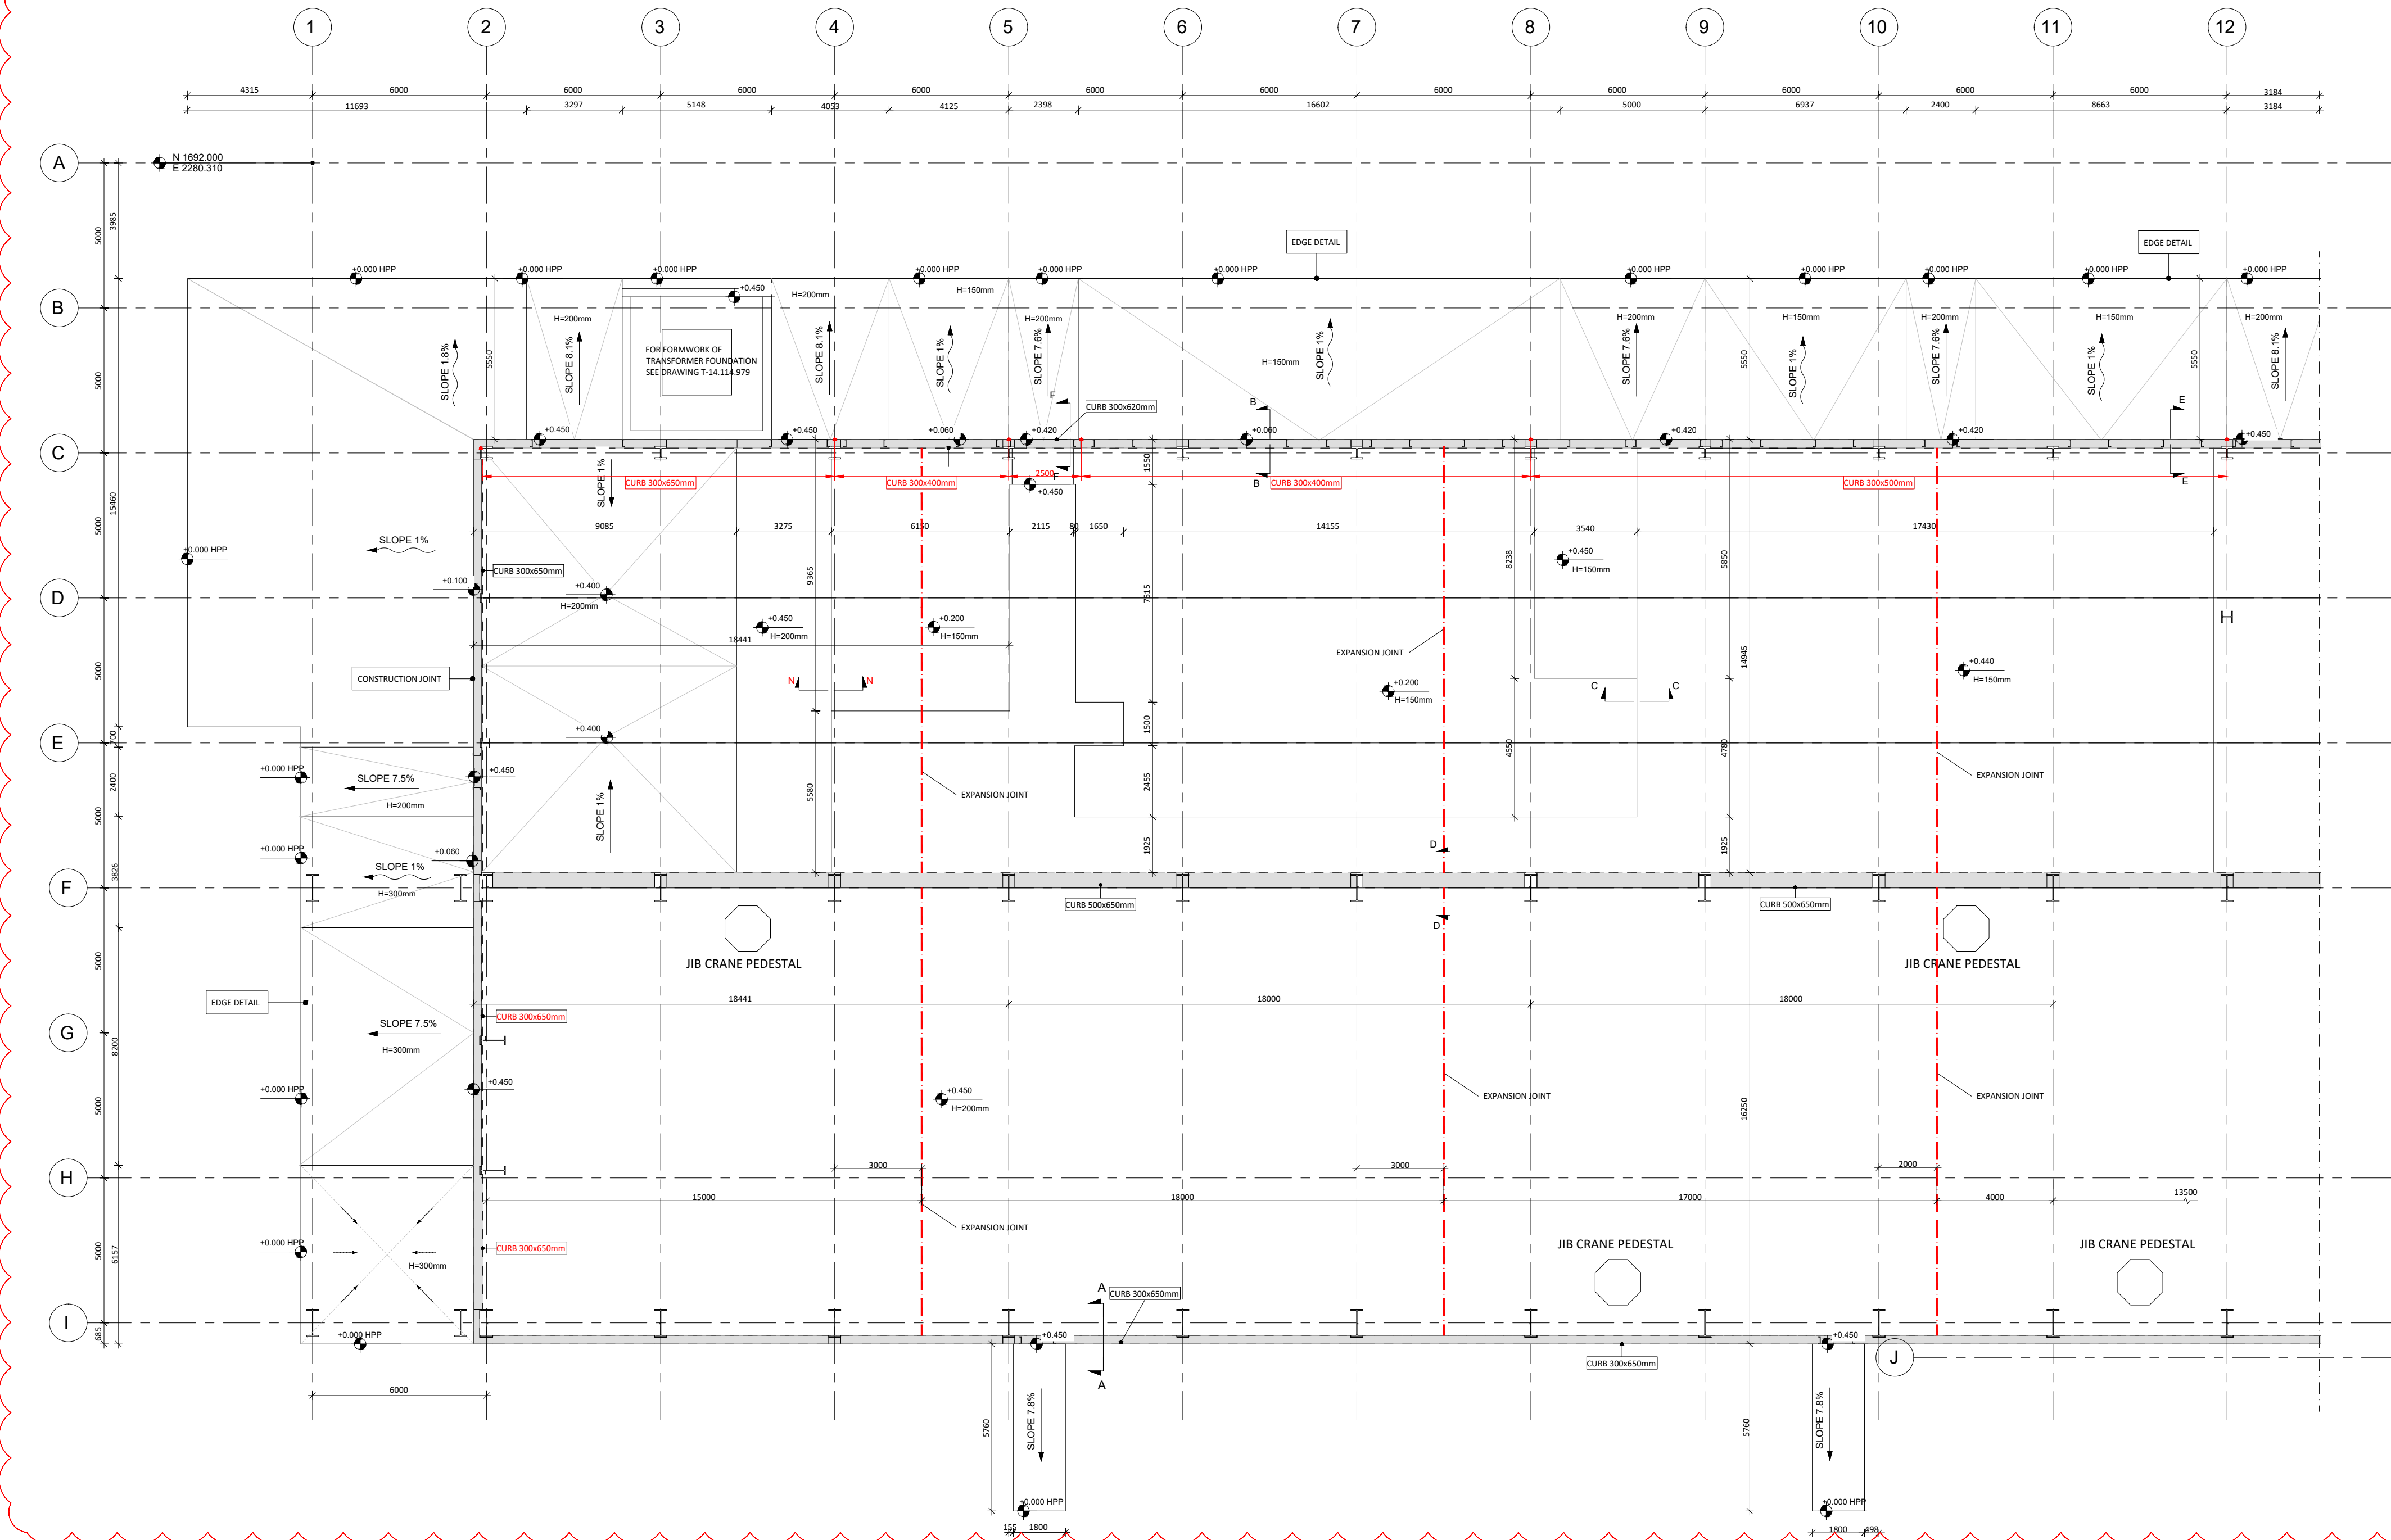

SECTION A-A

1:50

SECTION B-B

1:50

SECTION C-C

1:50

SECTION D-D

1:50

SECTION E-E



1:50

SECTION F-F

1:50

EDGE DETAIL

1:5

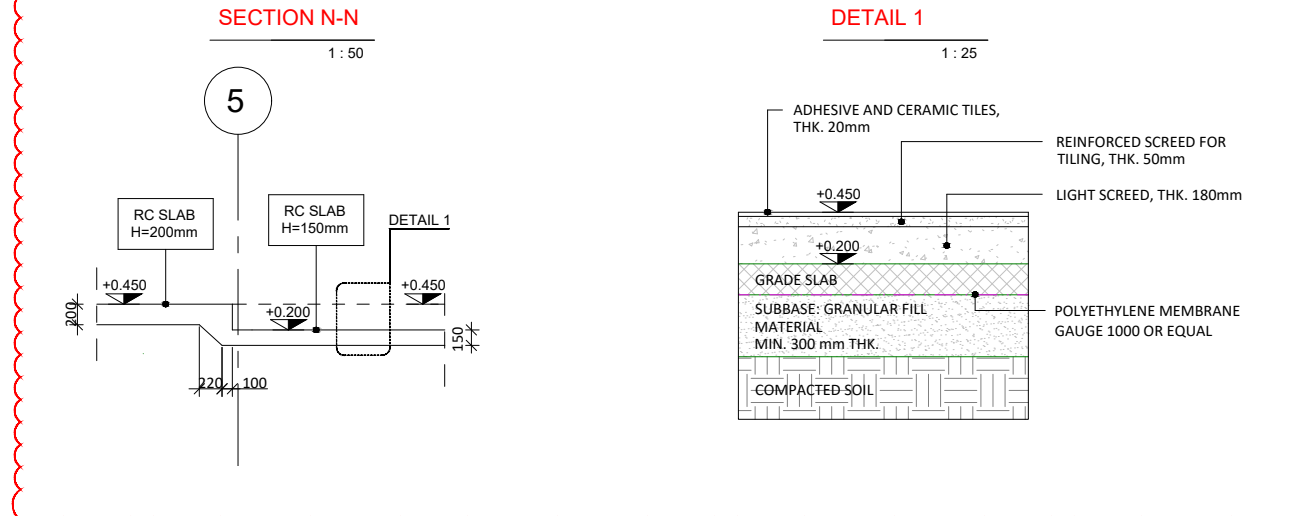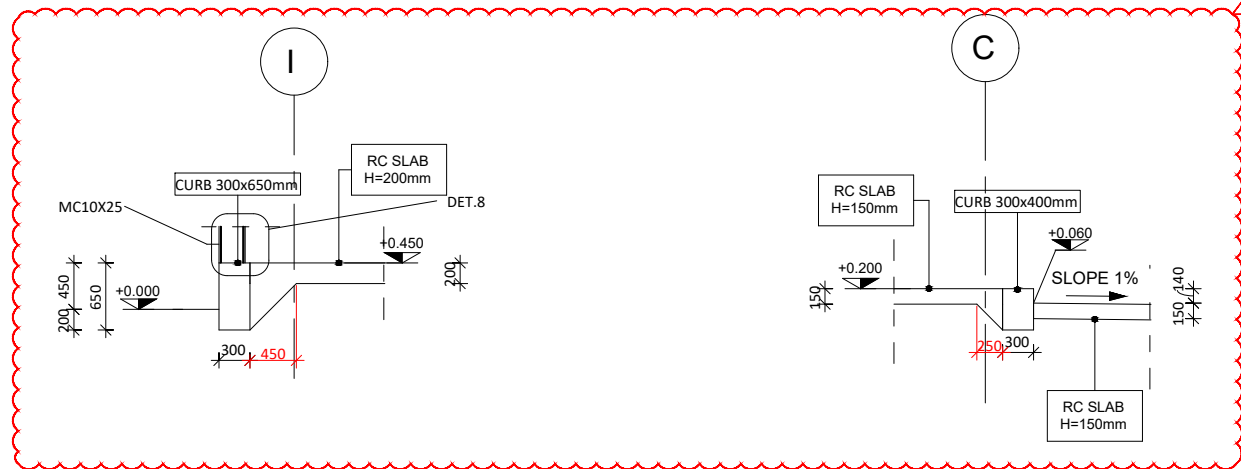

NOTES

THIS DRAWING IS TO BE READ IN CONJUNCTION WITH

DOCUMENT NO.	DRAWING TITLE
T-14.114.944	T7 MAINTENANCE WORKSHOP - CONCRETE GRADE SLAB - REINFORCEMENT
T-14.114.945	T7 MAINTENANCE WORKSHOP - CONCRETE GRADE CHILLER AREA - FORMWORK AND REINFORCEMENT
T-14.114.947	T7 MAINTENANCE WORKSHOP - CONCRETE GRADE FOR OUTSIDE - LAY-DOWN AREAS - FORMWORK AND REINFORCEMENT
T-14.111.000	CIVIL WORKS DESIGN CRITERIA
T-14.112.000	CONCRETE WORKS GENERAL NOTES
T-14.110.445	T7 MAINTENANCE WORKSHOP - STRUCTURAL CALCULATION REPORT FOR CONCRETE STRUCTURES
T-14.143.101-SH1	TYPICAL LIGHTING & LIGHTNING INSTALLATION DRAWINGS - UNIT 4000 ELECTRICITY GENERATION SYSTEM
T-14.140.363-SH1	NEW WORKSHOP ELECTRICAL ROOM EARTHING LAYOUT UNIT 0000 - GENERAL FACILITIES
T-14.114.970 (1/1)	BASE PLATES WITH EMBEDDED ANCHOR BOLTS

GENERAL NOTES

- 1) ALL DIMENSIONS ARE IN MILLIMETRES
- 2) ALL COORDINATES AND ELEVATIONS ARE IN METERS AND REFER TO PLANT DATUM
- 3) FIXED LEVEL 100.000 = +3.60m MSL
- 4) REFERENCE ELEVATION +0.000 HPP = 99.800 = +3.40m MSL
- 5) ELECTRICAL EARTHING INSTALLATION DETAIL SHALL BE AS PER: T-14.143.101-SH1 TYPICAL EARTHING & LIGHTNING INSTALLATION DRAWINGS - UNIT 4000 ELECTRICITY GENERATION SYSTEM
- 6) ERTPLANE EARTHING/GROUND LAYOUT AREA AND UNDERGROUND SHALL BE AS PER: T-14.140.363-SH1-Q NEW WORKSHOP ELECTRICAL ROOM EARTHING LAYOUT UNIT 0000 - GENERAL FACILITIES

ABBREVIATIONS


BOB	BOTTOM OF BEAM
BOF	BOTTOM OF FOUNDATION
CMU	CONCRETE MASONRY UNIT
F.F.L	FINISHED FLOOR LEVEL
HPP	HIGH POINT PAVEMENT
M.S.L	MEAN SEA LEVEL
RC	REINFORCED CONCRETE
TOR	TOP OF BEAM
TCC	TOP OF CONCRETE
TOP	TOP OF FOUNDATION
TOP	TOP OF PARAPET
TOP	TOP OF PEDESTAL
TOR	TOP OF ROOF

LEGEND

---	EXPANSION JOINT
-----	-----------------

THE CONTENTS OF THIS DRAWING REPLACE THE DELETED DOC: T-14.114.943 - "T7 MAINTENANCE WORKSHOP - CONCRETE GRADE SLAB - FORMWORK - PART2"

KEY PLAN

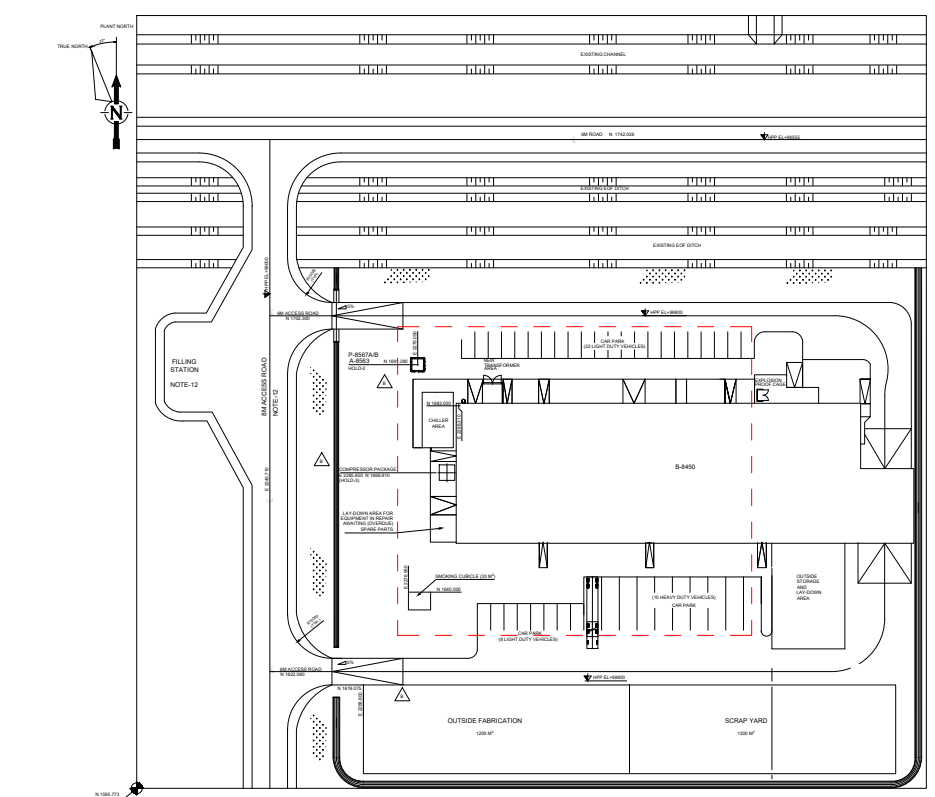

CWP NO: B05-WP7.2-150-BM-BA-102

REV	DESCRIPTION	DATE	CHKD	DATE	APPD	DATE
AB.F3	FDC - NLNG7 - SCJW - CIV - 0470_0A	05/11/20	DE	23/03/24	SFA	23/03/24
AB.F2	FDC - NLNG7 - SCJW - CIV - 0470_0	05/11/20	DE	09/04/24	DE	09/04/24
AB	APPROVED FOR CONSTRUCTION	05/11/20	DE	23/03/23	EE	23/03/23
AA	APPROVED FOR CONSTRUCTION	05/11/20	DE	13/02/23	EE	13/02/23
A	APPROVED FOR CONSTRUCTION WITH HOLDS	05/11/20	DE	27/05/22	EE	27/05/22
D	ISSUE FOR REVIEW	05/11/20	DE	05/11/20	CV	05/11/20
REV	DESCRIPTION	DATE	CHKD	DATE	APPD	DATE

This Document is confidential. The copyright therein is vested in Nigeria LNG Ltd, Nigeria. Recipient must obtain the written authority of the said company before wholly or partially duplicating. All rights reserved.

DATE: 05/11/20	CHECKED: EE	DATE: 05/11/20	APPROVED: CV	DATE: 05/11/20	APPROVED: CV
DATE: 05/11/20	APPROVED: CV	DATE: 05/11/20	APPROVED: CV	DATE: 05/11/20	APPROVED: CV
DATE: 05/11/20	APPROVED: CV	DATE: 05/11/20	APPROVED: CV	DATE: 05/11/20	APPROVED: CV
NIGERIA LIQUEFIED NATURAL GAS
NLNG - BONNY


LOCATION: BONNY ISLAND, NIGERIA
PROJECT: T7 MAINTENANCE WORKSHOP
CONCRETE GRADE SLAB - FORMWORK

CONTRACTOR DRAWING NO: 1084-CE-A-14942
SCALE: VAR

COMPANY PROJECT NO: B1901700R
CONTRACTOR PROJECT NO: 14942R

COMPANY DRAWING NO: T-14.114.942
SHEET: 1/2
REV: AB.F3

ADVANCE COPY

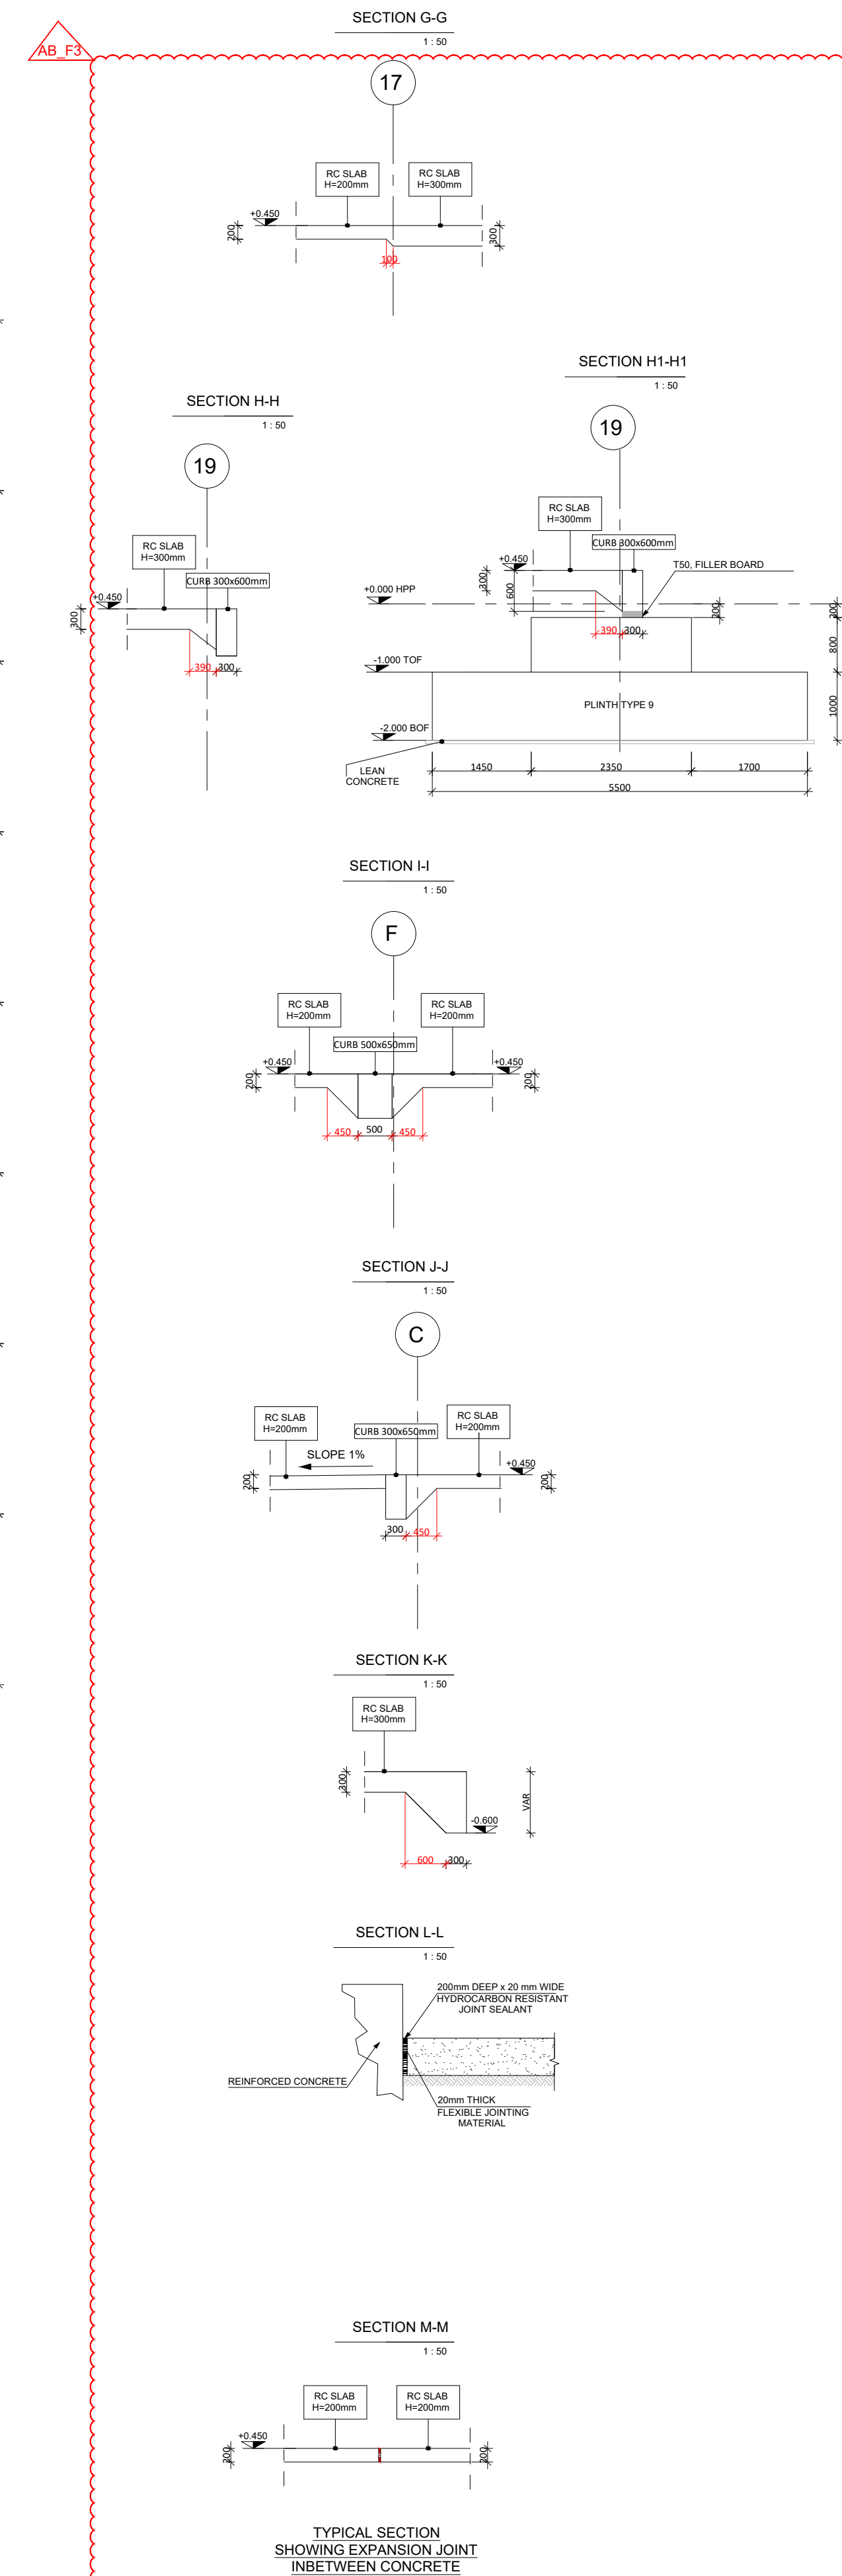

This document is confidential. The copyright therein is vested in Nigeria LNG Ltd, Nigeria. This document must obtain the written authority of the said company before wholly or partially duplicating. All rights reserved.				
DRAWN: OE DATE: 05/11/2020 CHECKED: EE DATE: 05/11/2020 APPROVED: CV DATE: 05/11/2020 PREP. LING:		 NIGERIA LIQUEFIED NATURAL GAS NLNG - BONNY  Shell NIGERIA  DMEWASCO DMEWASCO		
PROJECT: NLNG TRAIN 7 LOCATION: BONNY ISLAND, NIGERIA TITLE: T7 MAINTENANCE WORKSHOP CONCRETE GRADE SLAB – FORMWORK		DRAWING NO: CIV SHEET NO: 8400		
CONTRACTOR DRAWING NO: 1084-CE-A-10492		CONTRACTOR PROJECT NO: T-14.114.942		
SCALE: VAR		SHEET: 2/2		
REV:		REV: AS_FJ		