




GRADE SLAB REINFORCEMENT PLAN - A

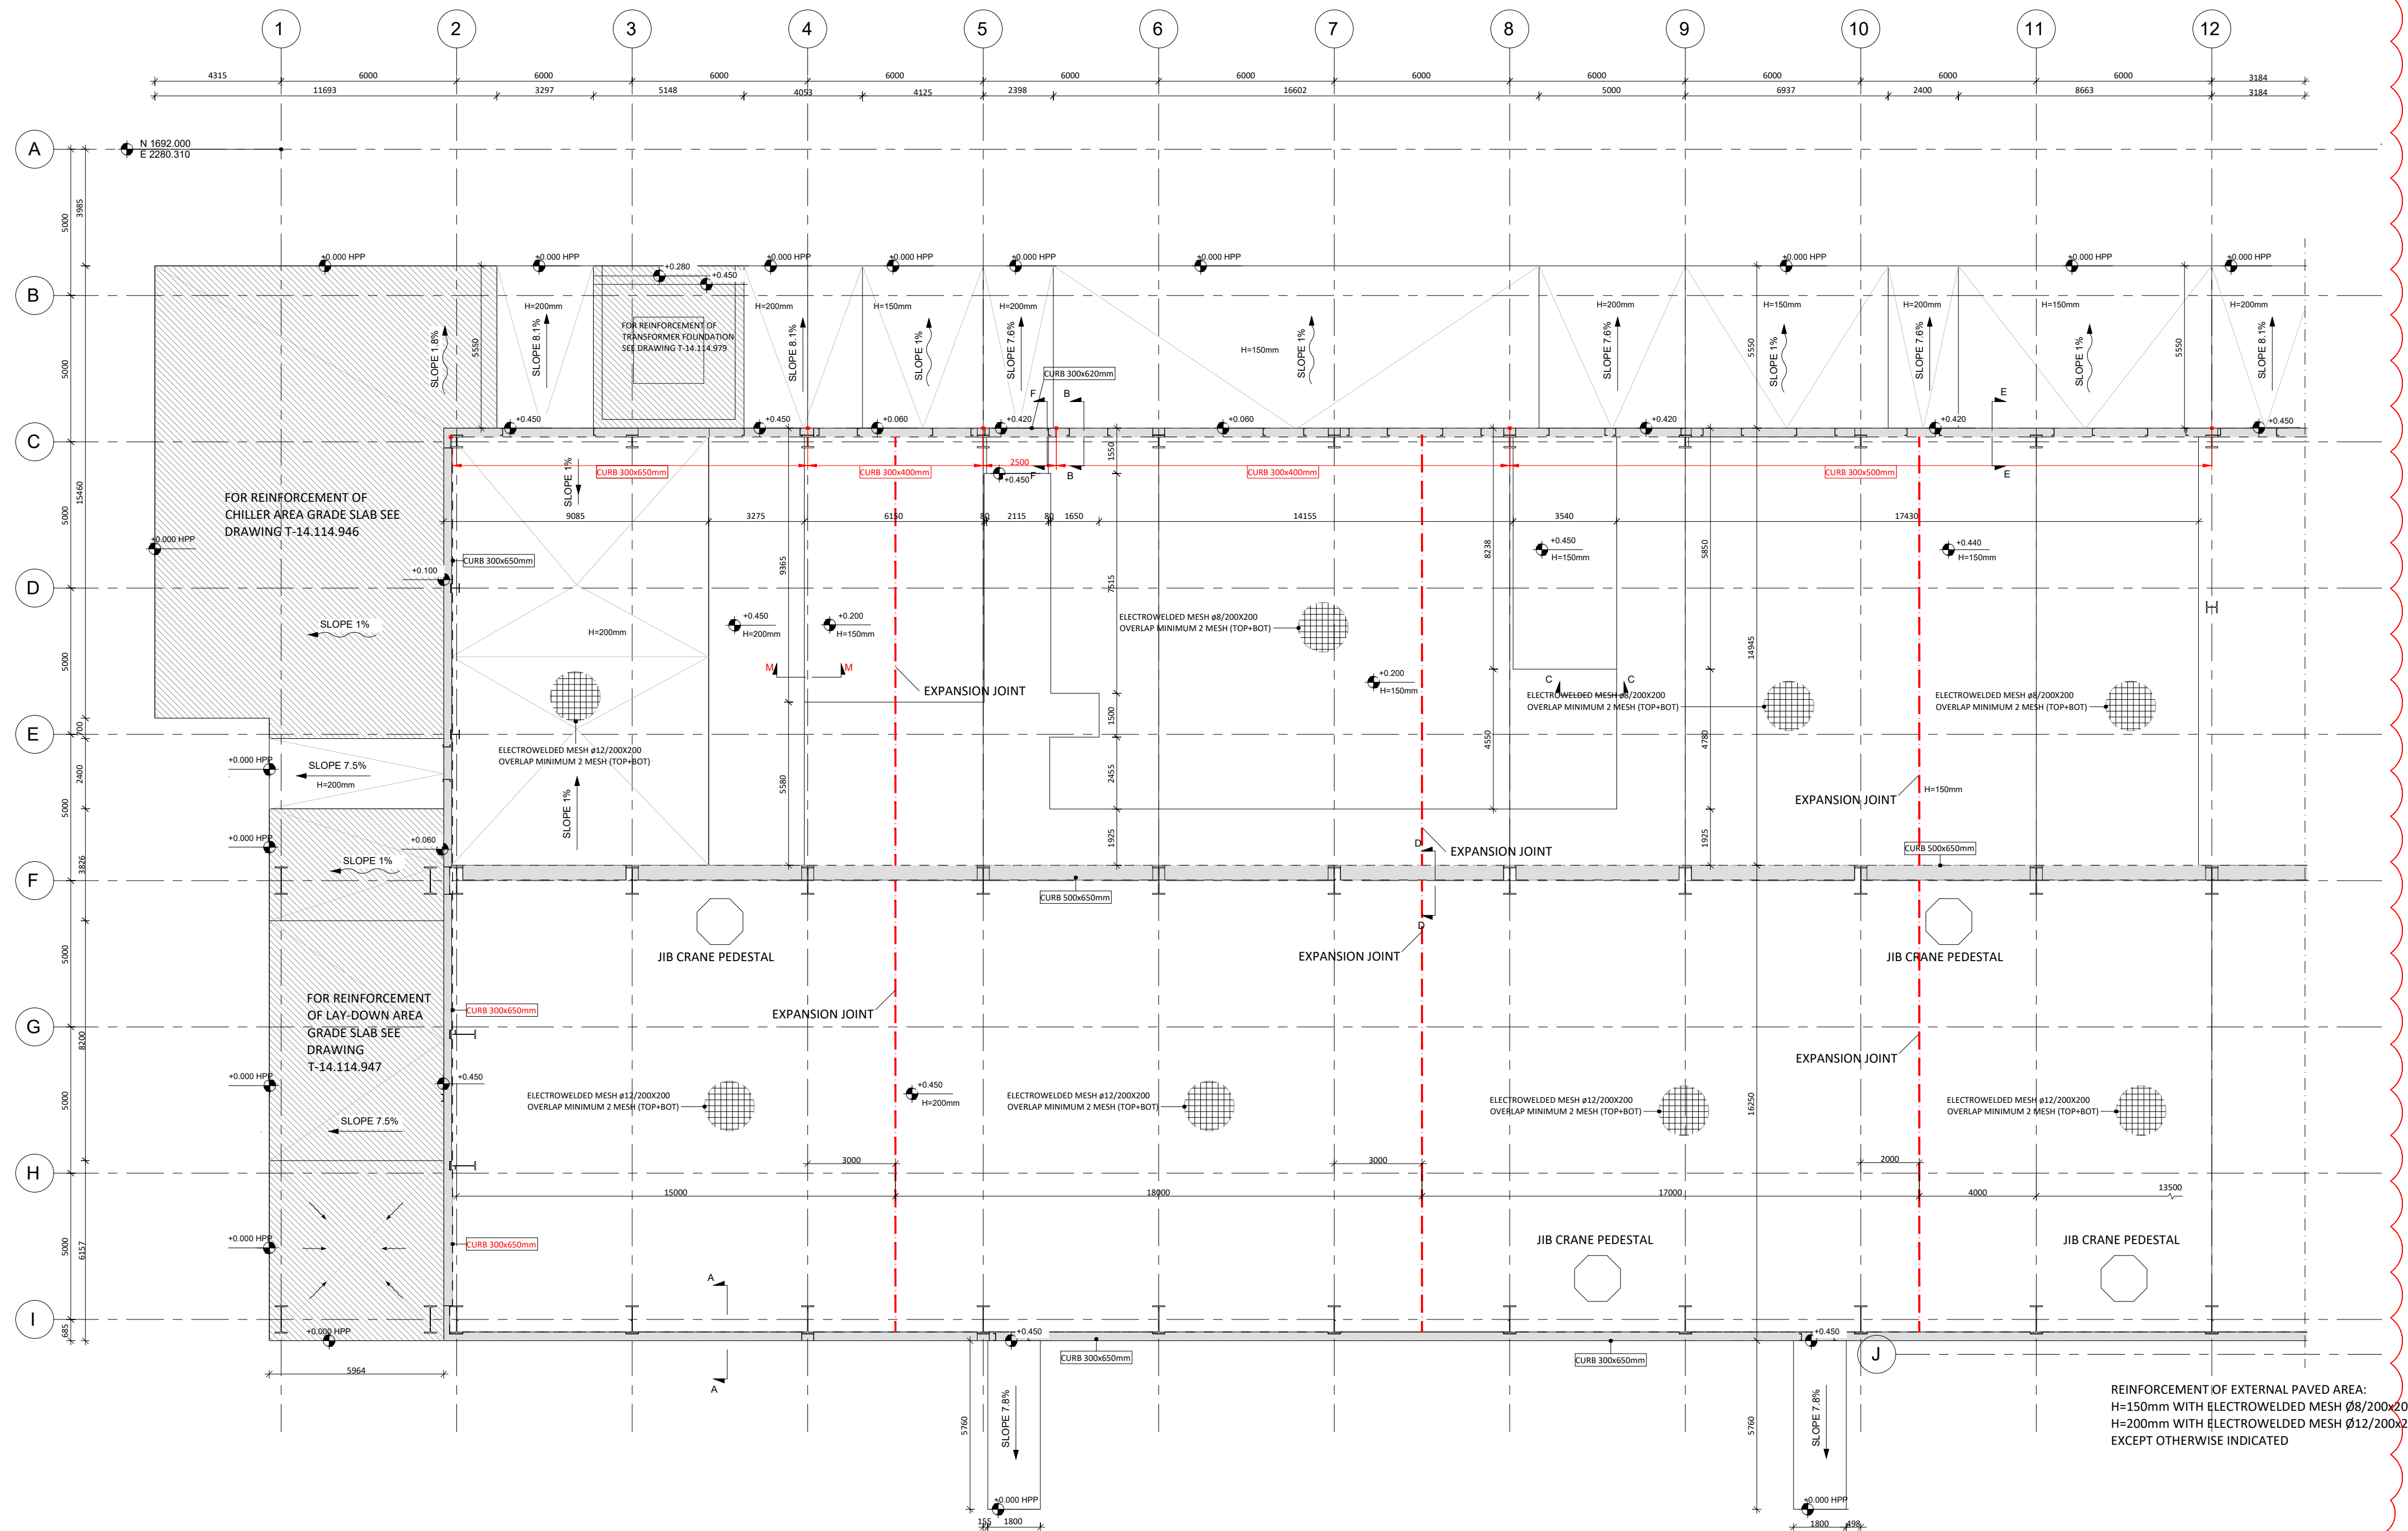


SECTION A-A
1:50

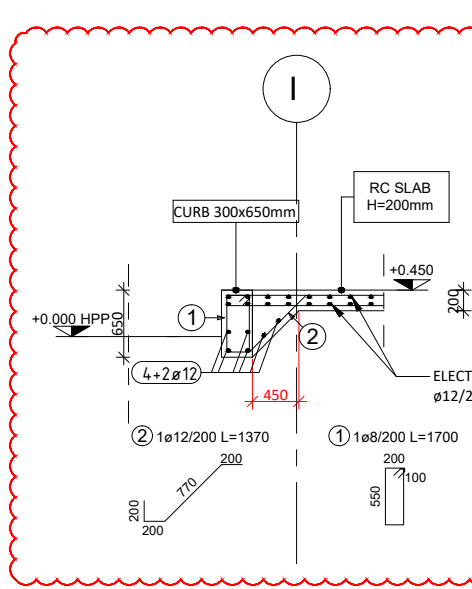


SECTION B-B
1:50

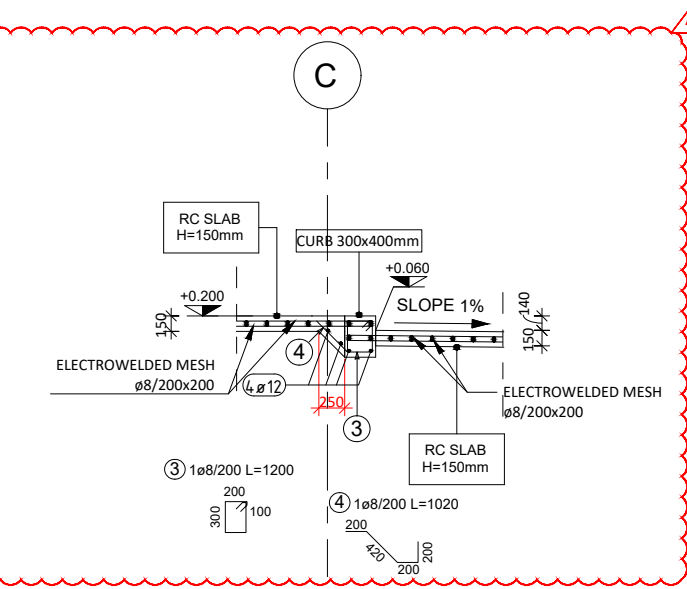


SECTION C-C
1:50

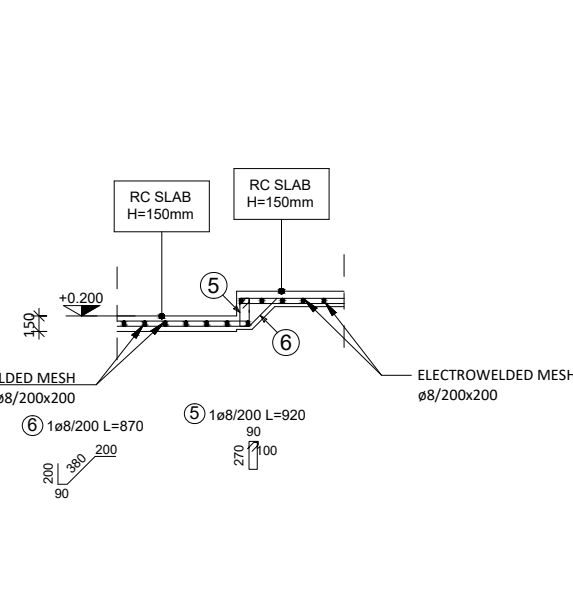


SECTION D-D
1:50

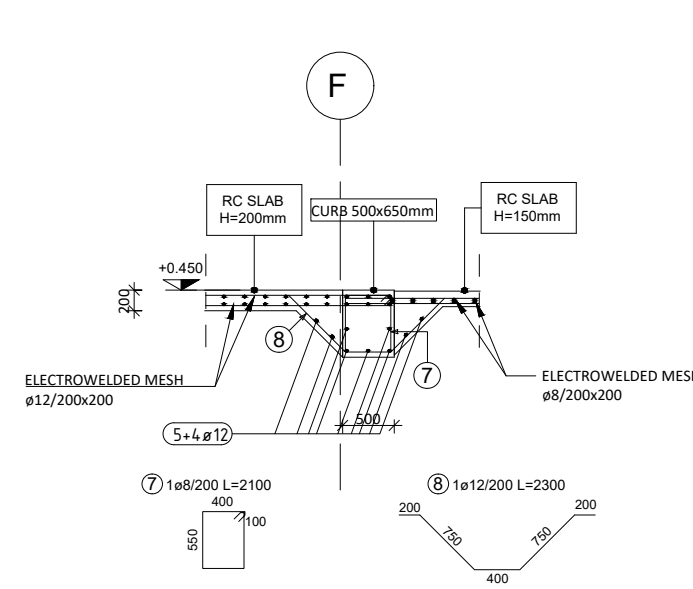


SECTION E-E
1:50

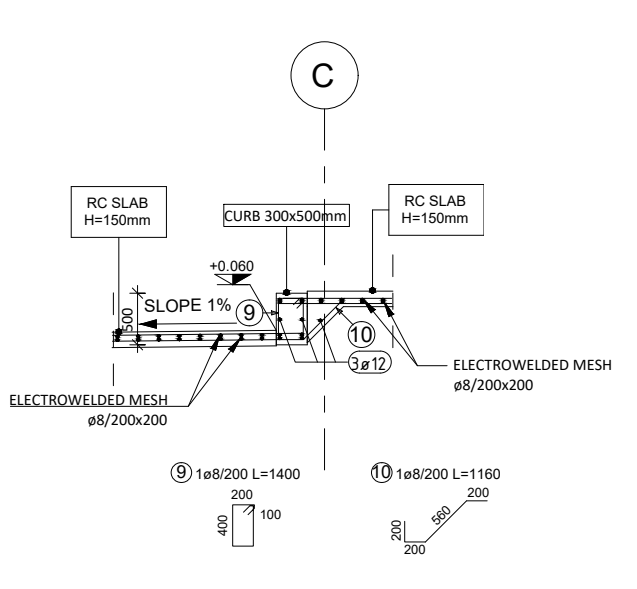

SECTION F-F
1:50

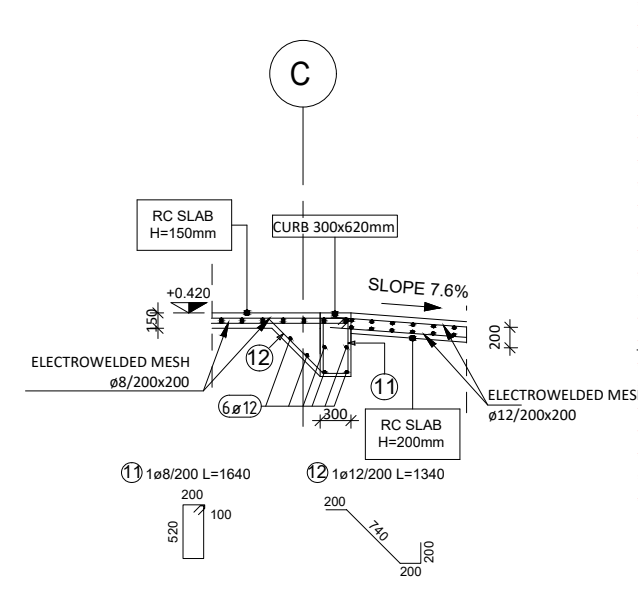

SECTION M-M
1:50

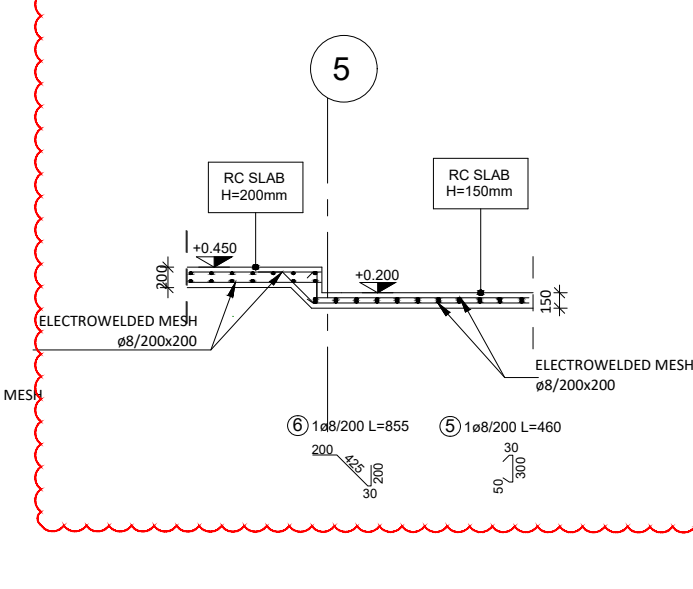

NOTES

THIS DRAWING IS TO BE READ IN CONJUNCTION WITH

DOCUMENT NO.	DRAWING TITLE
T-14.114.942	T7 MAINTENANCE WORKSHOP - CONCRETE GRADE SLAB - FORMWORK
T-14.114.943	T7 MAINTENANCE WORKSHOP - CONCRETE GRADE CHILLER AREA - FORMWORK AND REINFORCEMENT
T-14.114.947	T7 MAINTENANCE WORKSHOP - CONCRETE GRADE FOR OUTSIDE - LAY-DOWN AREAS - FORMWORK AND REINFORCEMENT
T-14.114.948	T7 MAINTENANCE WORKSHOP - EXPLOSION PROOF CAGES - FORMWORK - REINFORCEMENT
T-14.114.939	T7 MAINTENANCE WORKSHOP - TRANSFORMERS - BLDG. FOUNDATION - FORMWORK - REINFORCEMENT
T-14.112.000	CONCRETE WORKS GENERAL NOTES
T-14.112.000	TYPICAL EARTHING & LIGHTNING INSTALLATION DRAWINGS - UNIT 4000 ELECTRICITY FOUNDATION SYSTEM
T-14.140.943-SH1	NEW WORKSHOP ELECTRICAL ROOM EARTHING LAYOUT UNIT 0000 - GENERAL FACILITIES

GENERAL NOTES

- ALL DIMENSIONS ARE IN MILLIMETRES.
- ALL COORDINATES AND ELEVATIONS ARE IN METERS AND REFER TO PLANT DATUM
- FINED LEVEL 100.000 + 3.60m MSL
- REFERENCE ELEVATION +0.000 (HPP) = 99.800 + 3.40m MSL
- ELECTRICAL EARTHING INSTALLATION DETAIL SHALL BE AS PER: T-14.140.943-SH1-TYPICAL EARTHING & LIGHTNING INSTALLATION DRAWINGS - UNIT 4000 ELECTRICITY FOUNDATION SYSTEM
- KEYPLANE EARTH/GROUND LAYOUT AREA AND UNDERGROUND SHALL BE AS PER: T-14.140.943-SH1-TYPICAL EARTHING LAYOUT UNIT 0000 - GENERAL FACILITIES
- ELECTROWELDED MESH TERMINATES AT THE EXTENT OF CURB

ABBREVIATIONS


- BOB BOTTOM OF BEAM
BOF BOTTOM OF FOUNDATION
CMU CONCRETE MASONRY UNIT
FEL FINISHED FLOOR LEVEL
HPP HIGH POINT PAVEMENT
MSL MEAN SEA LEVEL
RC REINFORCED CONCRETE
TOB TOP OF BEAM
TOC TOP OF CONCRETE
TOP TOP OF FOUNDATION
TOP TOP OF PARAPET
TOPD TOP OF PEDESTAL
TOR TOP OF ROOF

LEGEND

- EXPANSION JOINT


PROVIDE EXPANSION JOINTS SPACED NO MORE THAN 20m (65ft.) APART AND CONTRACTION JOINTS SPACED AT A MAXIMUM DISTANCE OF 8m IN BOTH WAYS ACCORDING TO T-14.111.000 AND DEP 34.13.20.31

CONCRETE COVER DETAIL

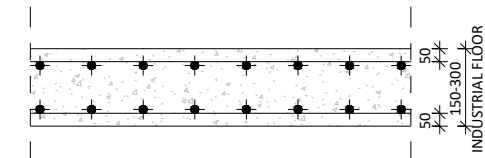

THE CONTENTS OF THIS DRAWING REPLACE THE DELETED DOC. T-14.114.945 - "T7 MAINTENANCE WORKSHOP - CONCRETE GRADE SLAB - REINFORCEMENT AND BARS BENDING SCHEDULE - PART 2"

KEY PLAN

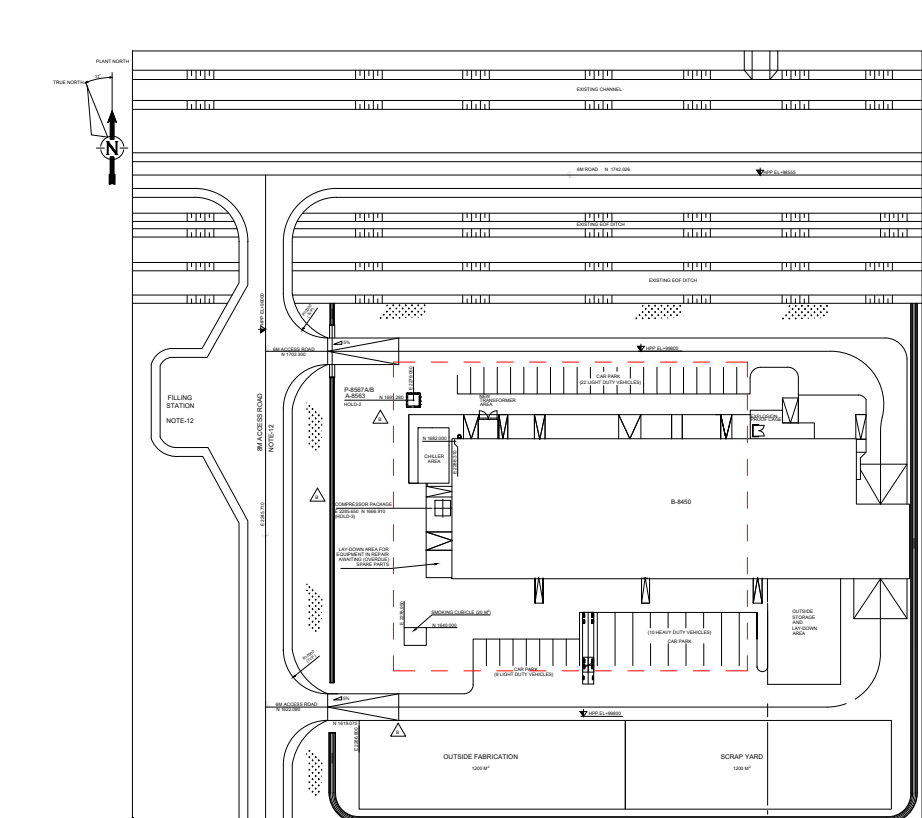


CWP NO: B05-WP7.2-150-BM-BA-102

REV	DESCRIPTION	OWN	DATE	CHKD	DATE	APPR	DATE
AB_F3	FDC - NUNGT7 - SCUV - CIV - 0470_0A	DSO	23/09/24	SFA	23/09/24	PIR	23/09/24
AB_F2	FDC - NUNGT7 - SCUV - CIV - 0470_0	DSO	09/04/24	OE	09/04/24	WPI	09/04/24
AB	APPROVED FOR CONSTRUCTION	OE	23/03/23	EE	23/03/23	CV	23/03/23
AA	APPROVED FOR CONSTRUCTION	OE	13/02/23	EE	13/02/23	CV	13/02/23
A	APPROVED FOR CONSTRUCTION WITH HOLDS	OE	27/05/22	EE	27/05/22	CV	27/05/22
D	ISSUE FOR REVIEW	OE	05/11/20	EE	05/11/20	CV	05/11/20

REVISIONS							
This Document is confidential. The copyright therein is vested in Nigeria LNG Ltd, Nigeria. Recipient must obtain the written authority of the said company before wholly or partially duplicating. All rights reserved.							
DATE:	05/11/20						
CHECKED:	EE						
DATE:	05/11/20	NIGERIA LIQUEFIED NATURAL GAS NLNG - BONNY					
APPROVED:	CV	NIG TRAIN 7					
DATE:	05/11/20	LOCATION: BONNY ISLAND, NIGERIA					
APPR. LNG:		SCALE: 1:100					
DATE:		CONTRACTOR DRAWING No. 1084-CE-A-14944					
SCALE:	VAR	COMPANY PROJECT No. B1901700P					
		CONTRACTOR PROJECT No. 14944					
		TITLE: T7 MAINTENANCE WORKSHOP CONCRETE GRADE SLAB - REINFORCEMENT					
		SHEET 1/2					
		REV AB_F3					

ADVANCE COPY

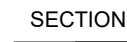GENERAL NOTES

ABBREVIATIONS


LEGEND

LEGEND

 EXPANSION JOINT

THE CONTENTS OF THIS DRAWING REPLACE THE DELETED DOC. T-14.114.945 - "T7 MAINTENANCE WORKSHOP - CONCRETE GRADE SLAB - REINFORCEMENT AND BARS BENDING SCHEDULE - PART2"


KEY PLAN

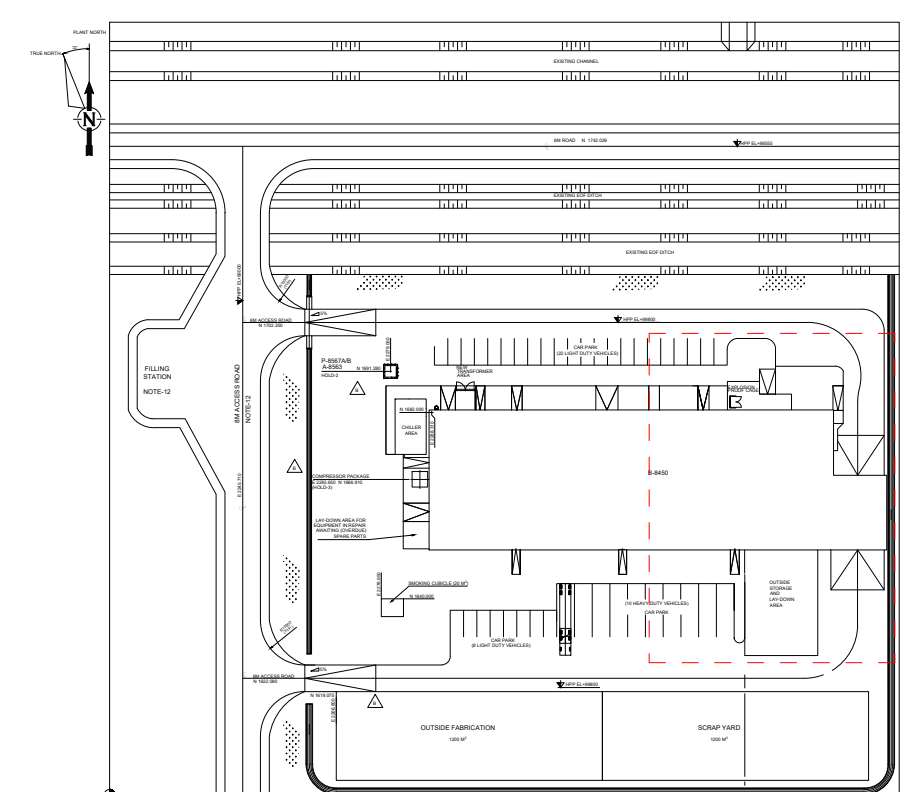

CWP NO: B05-WP7.2-150-BM-BA-102

AB_F3	FDC - NUNGIT-SCDJW-CIV-0470_0A	OSO	23/03/24	SFA	23/03/24	PIA	23/03/24
AB_F3	FDC - NUNGIT-SCDJW-CIV-0470_0	OSO	09/04/24	OE	09/04/24	MPJ	09/04/24
AB	APPROVED FOR CONSTRUCTION	OE	23/03/23	EE	23/03/23	CV	23/03/23
AA	APPROVED FOR CONSTRUCTION	OE	13/02/23	EE	13/02/23	CV	13/02/23
A	APPROVED FOR CONSTRUCTION WITH HOLDS	OE	27/05/22	EE	27/05/22	CV	27/05/22
0	ISSUE FOR REVIEW	OE	05/11/20	EE	05/11/20	CV	05/11/20
REV	DESCRIPTION	DWIV	DATE	CHKD	DATE	APPD	DATE

REVISIONS This Document is confidential. The copyright therein is vested in Nigeria LNG Ltd, Nigeria. Recipient must obtain the written authority of the said company before wholly or partially duplicating. All rights reserved.
--

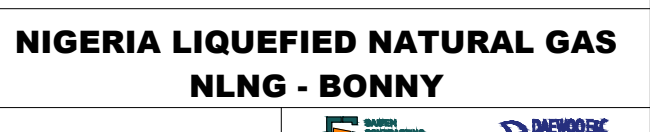

APPROVED: CV	KLING TRAIN /		
DATE: 05/11/20	LOCATION: DONNY ISLAND, NIGERIA	DISCIPLINE: CIV	INT. NO: 8400
APPRO. ENG:	TITLE: T7 MAINTENANCE WORKSHOP CONCRETE GRADE SLAB - REINFORCEMENT		
DATE:			
CONTRACTOR DRAWING NO: 1084-CE-A-14944			
SCALE: VAR	COMPANY PROJECT No.: 1084-CE-A-14944 CONTRACTOR PROJECT No.: 1084-CE-A-14944	COMPANY DRAWING NO.: T-14.114.944	SHEET: 2/2 REV: AR_F3